



CONCEPTUAL HOUSE PLANS


WITH BASEMENT

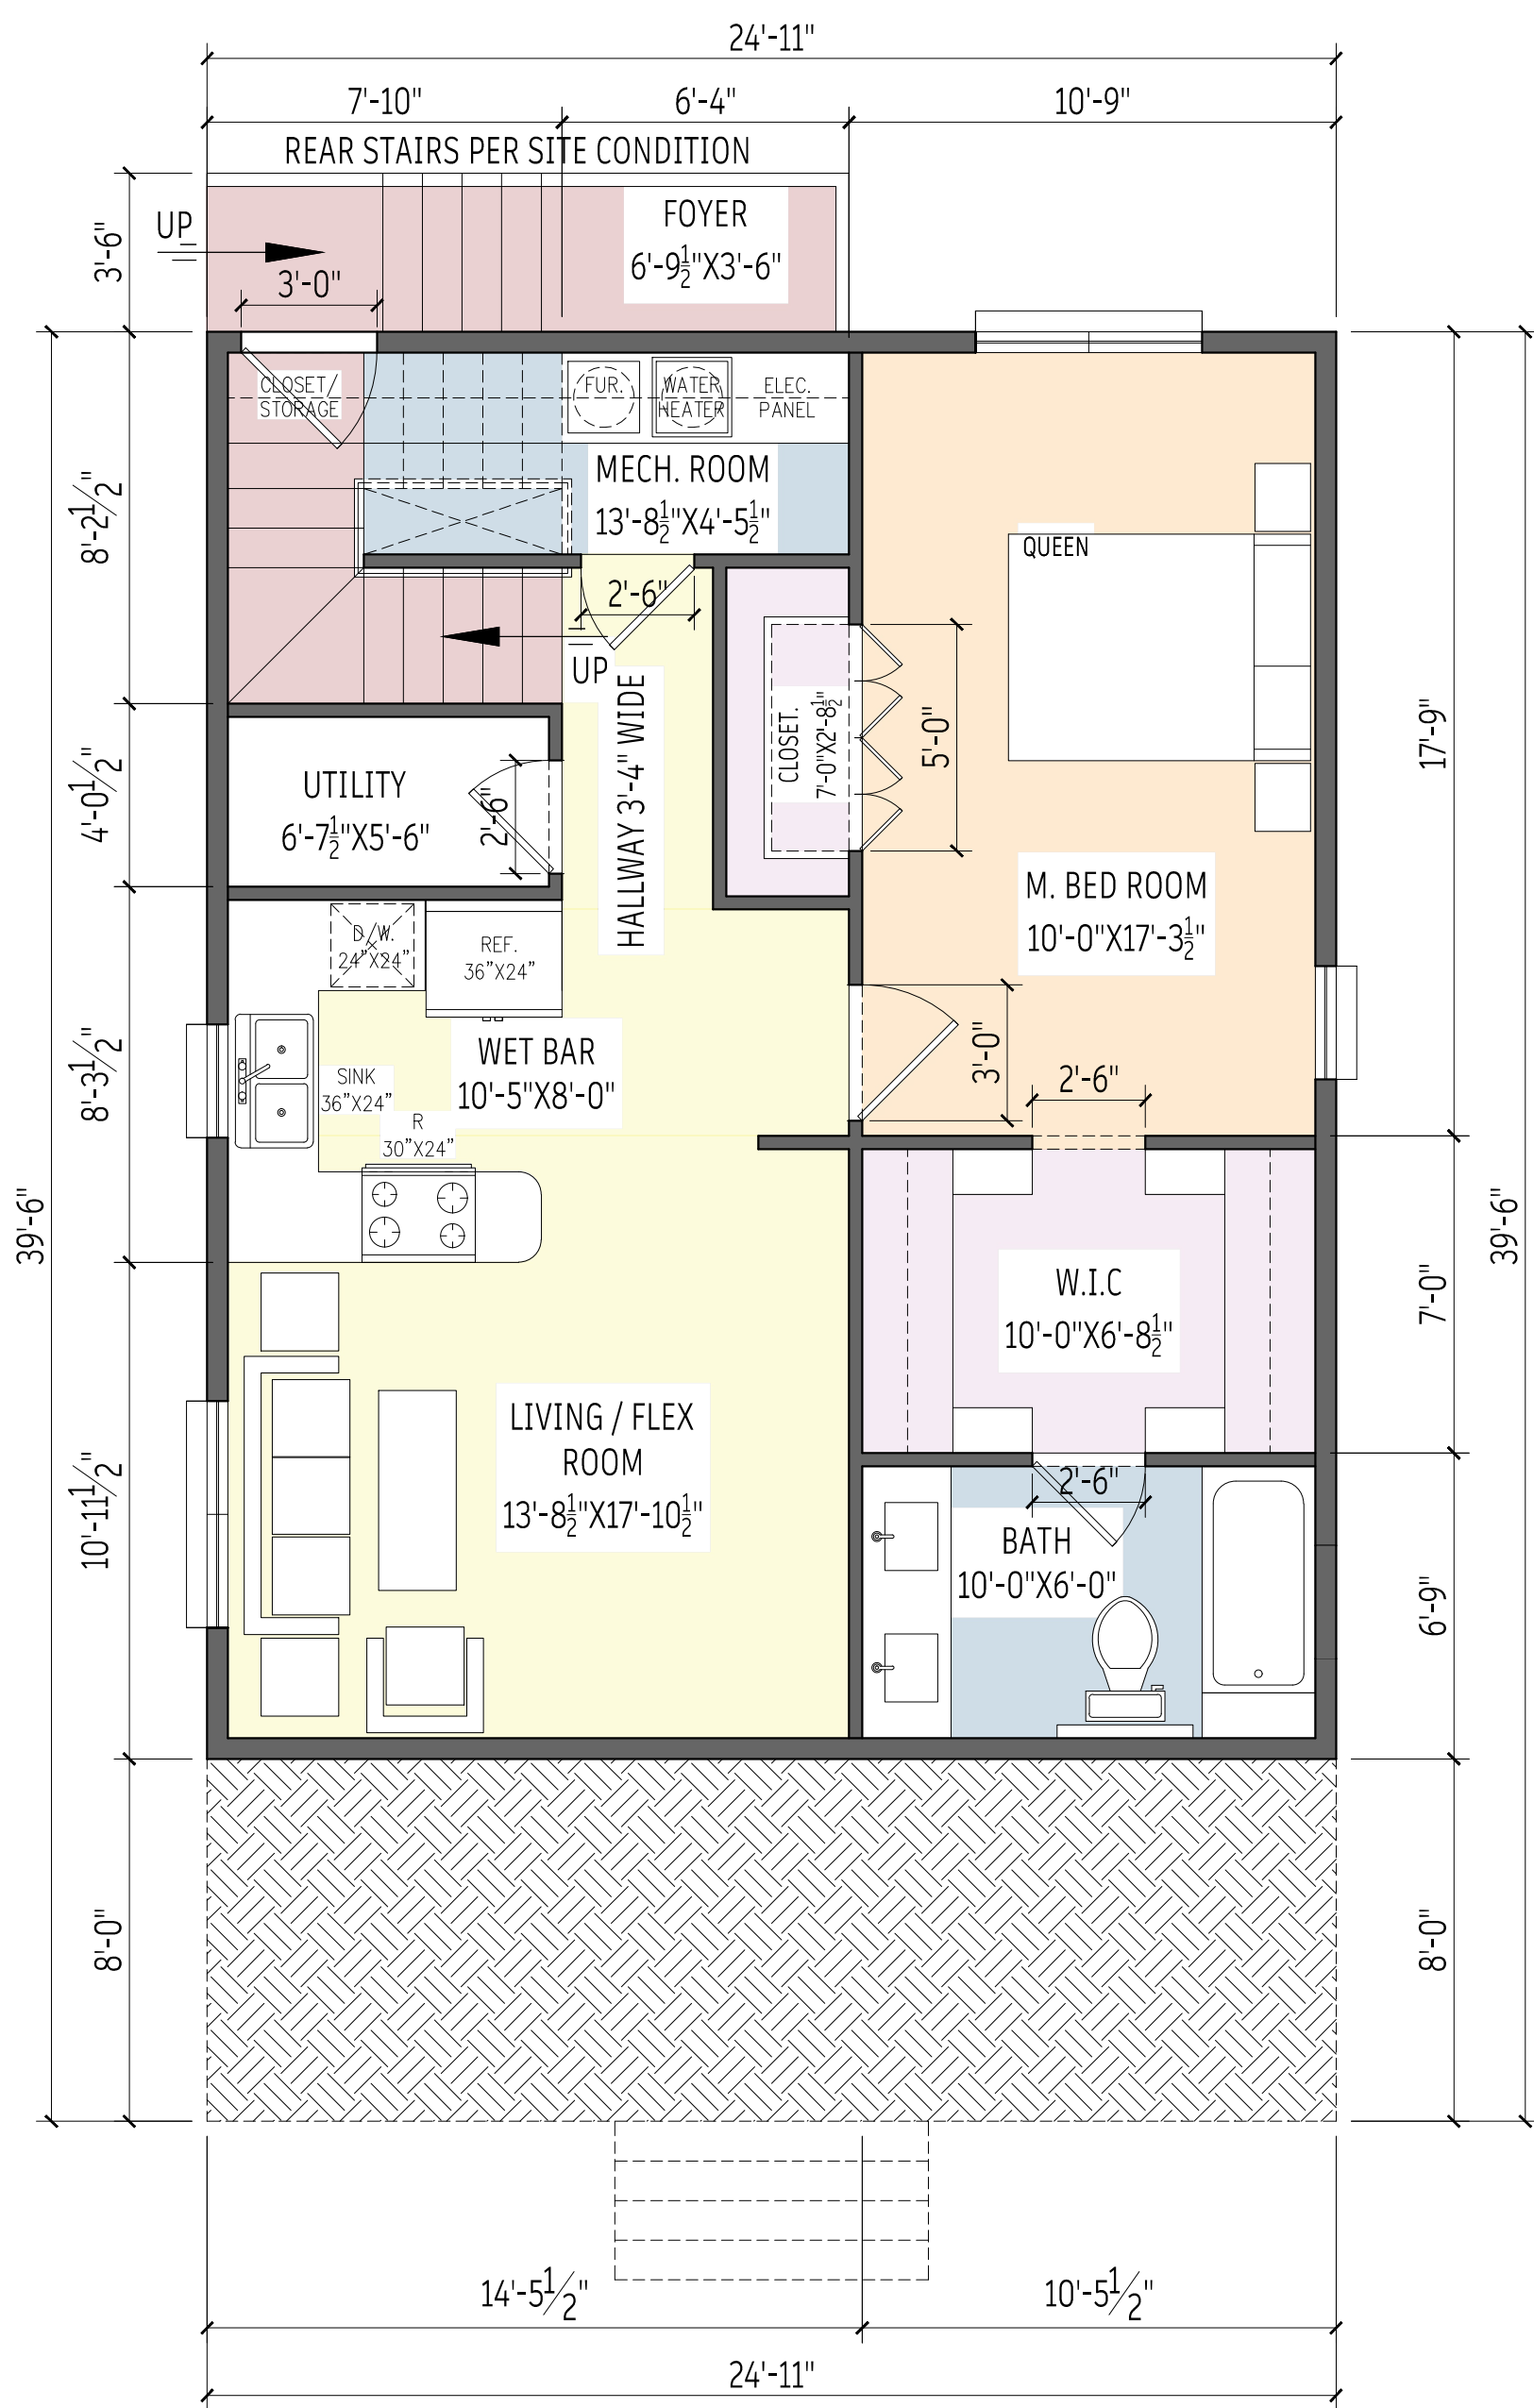

1 BASEMENT FLOOR PLAN.
Scale: 1/4" = 1'.0"

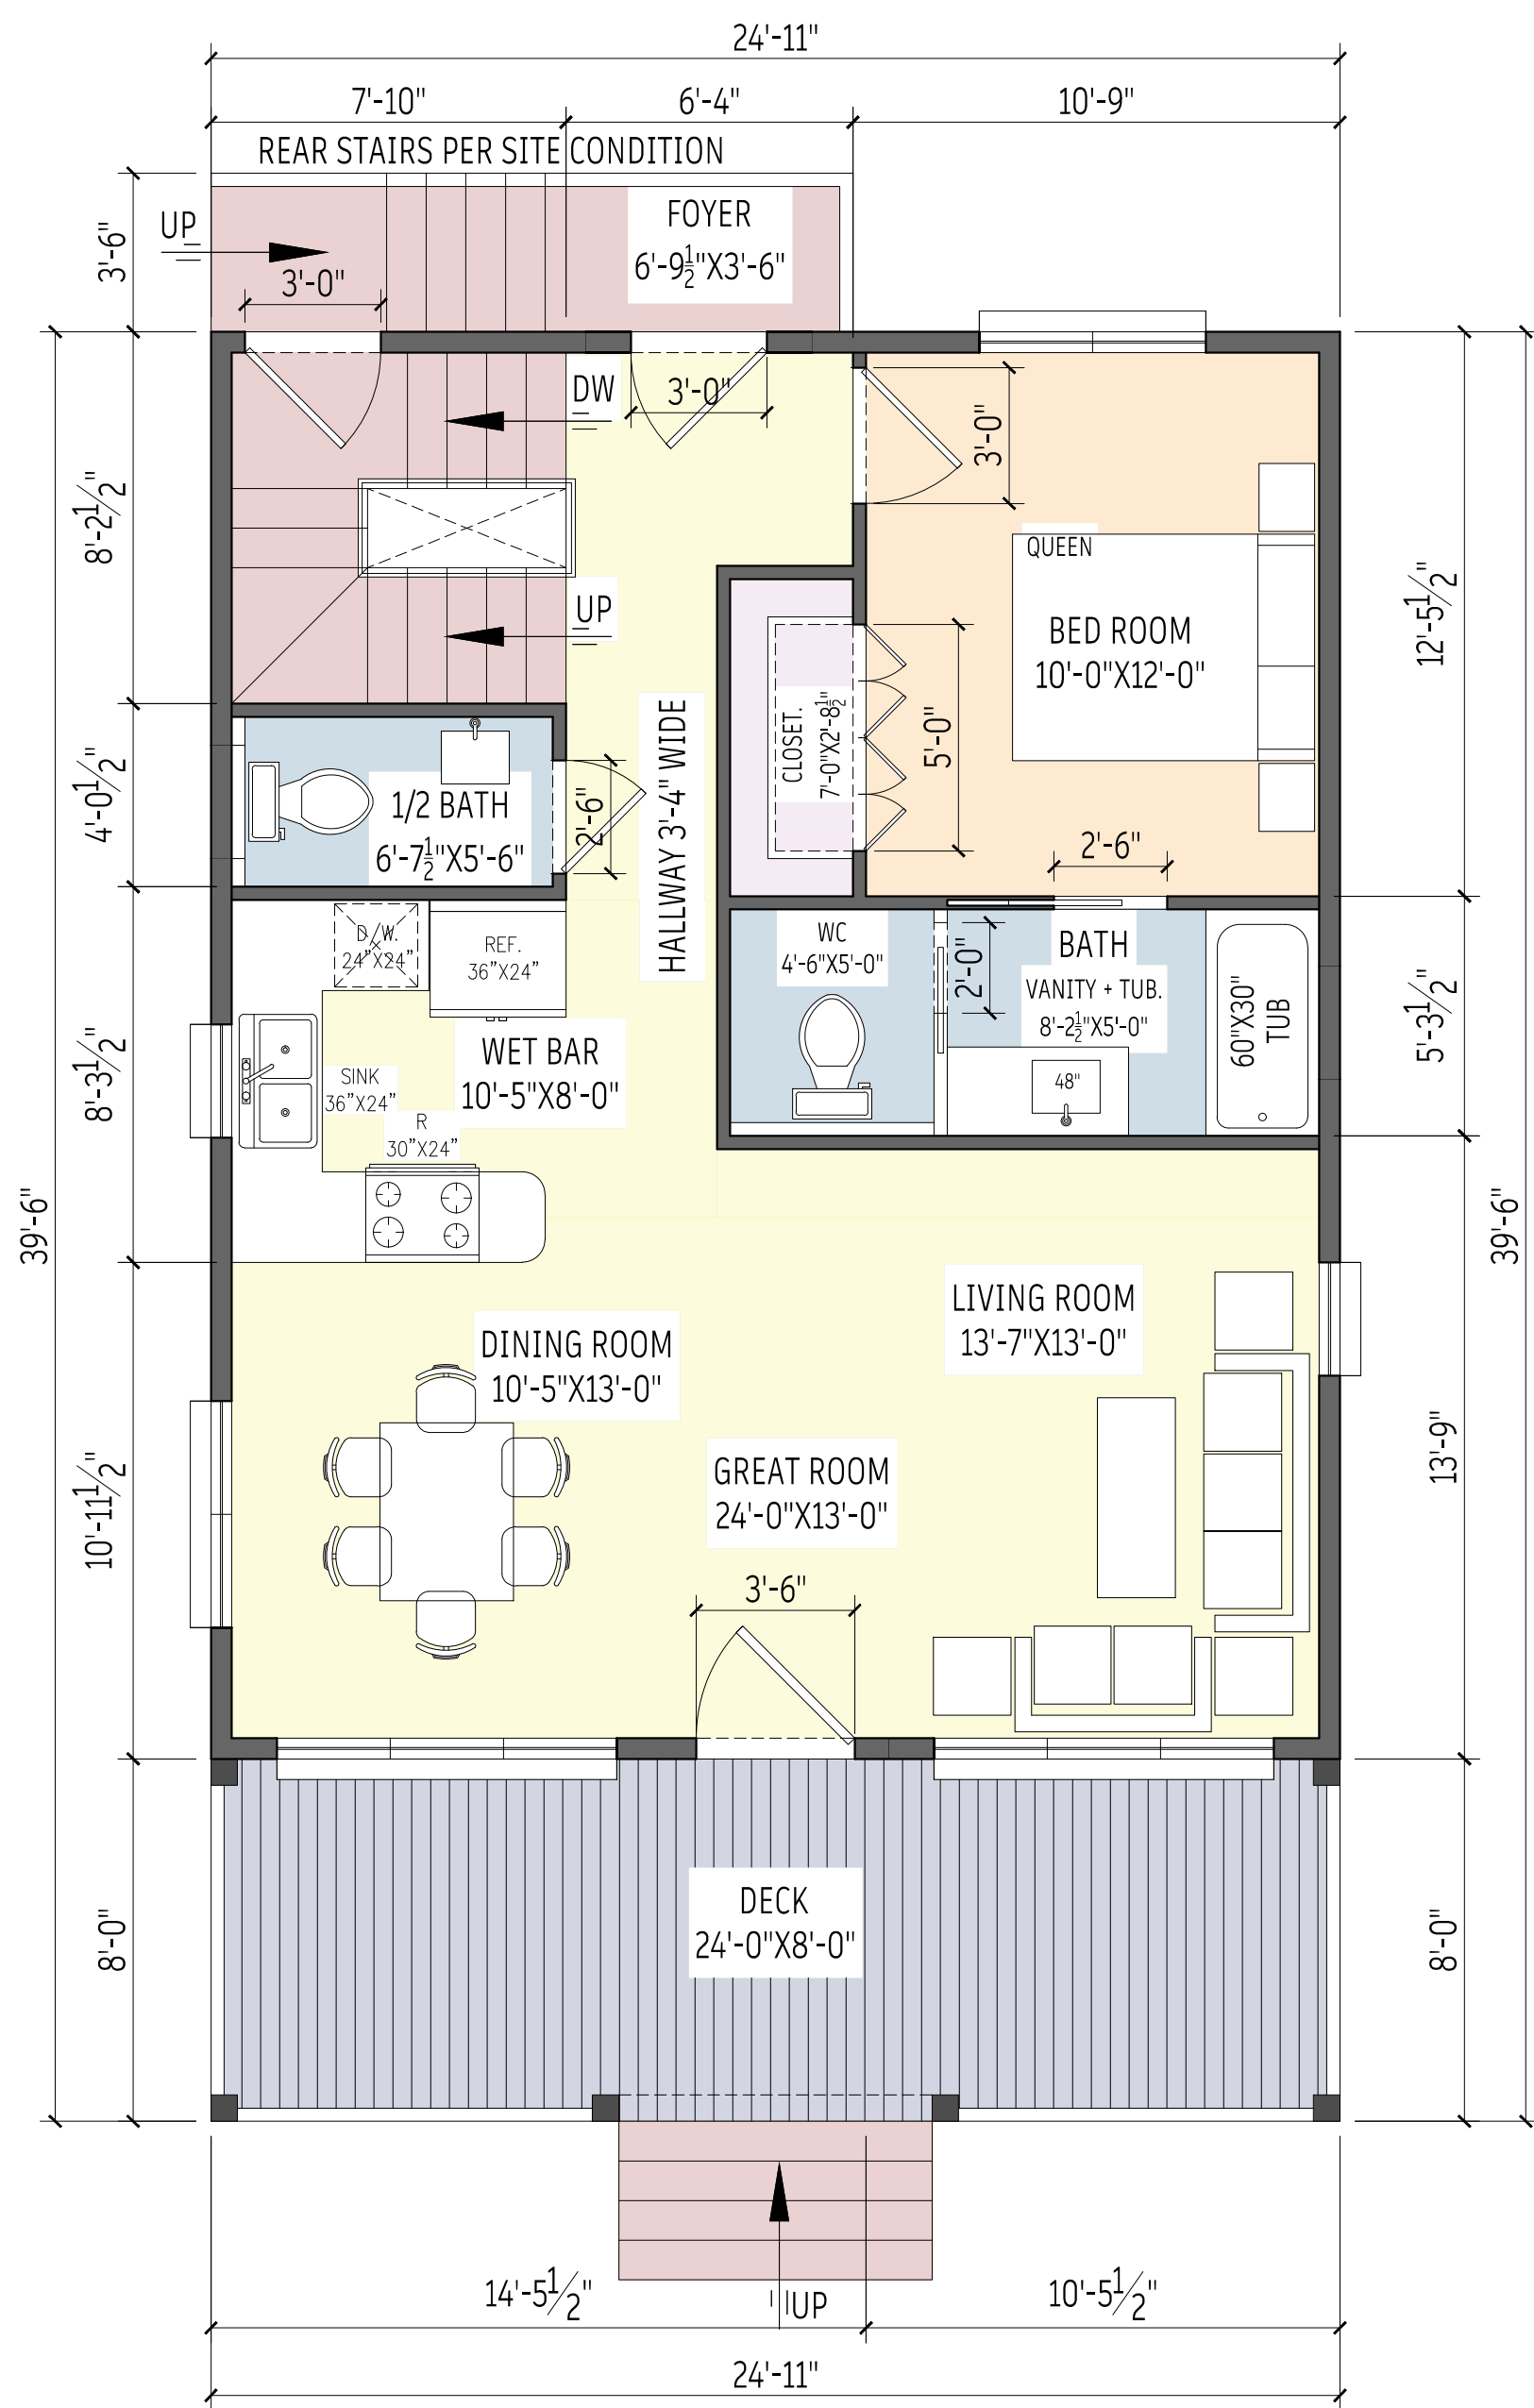

2 FIRST FLOOR PLAN.
Scale: 1/4" = 1'.0"

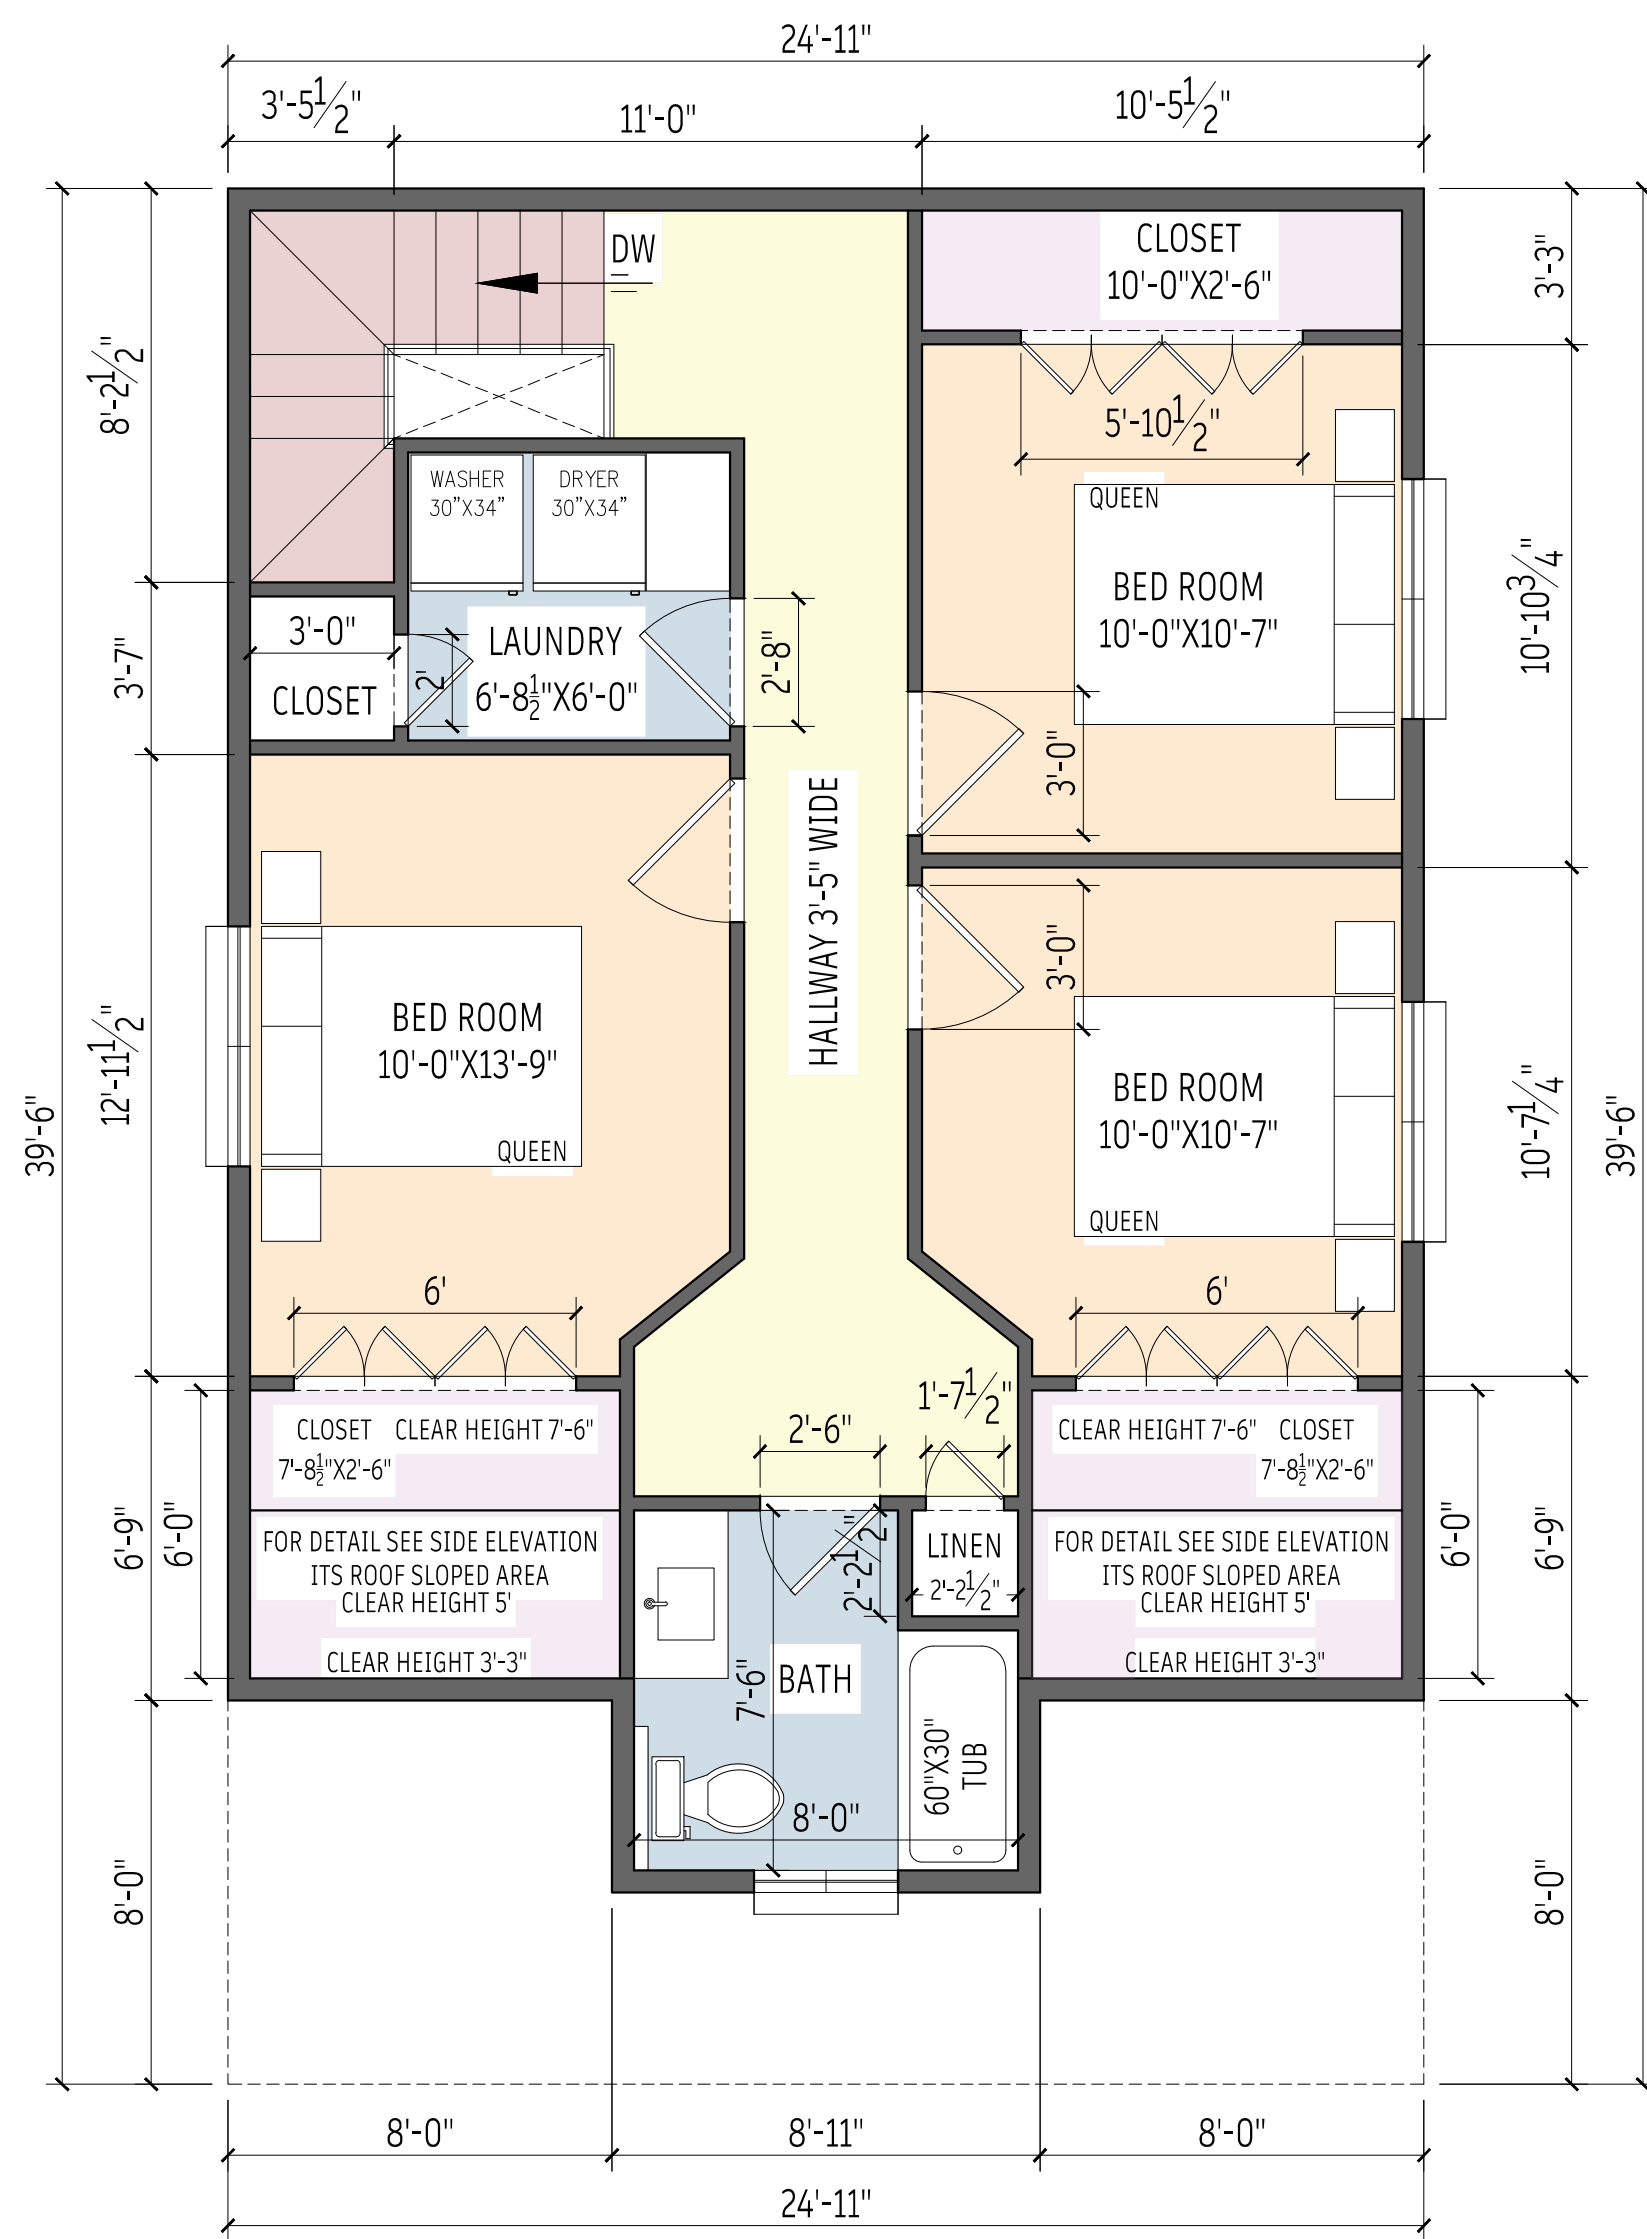

3 2ND FLOOR PLAN.
Scale: 1/4" = 1'.0"

COVERED AREA DETAILS.

- A. BASEMENT FLOOR PLAN**
- BASEMENT FLOOR HEATED AREA = 785 SFT.
 - TOTAL AREA UNDER ROOF = 785 SFT.
- B. FIRST FLOOR PLAN**
- ENTRANCE DECK (COVERED) = 200 SFT.
 - REAR FOYER (NOT COVERED) = 30 SFT.
 - FIRST FLOOR HEATED AREA = 785 SFT.
 - TOTAL AREA UNDER ROOF = 985 SFT.
- C. 2ND FLOOR PLAN**
- 2ND FLOOR HEATED AREA = 785 SFT.
 - TOTAL AREA UNDER ROOF = 785 SFT.
- TOTAL COVERED AREA (B.F. + FF + 2ND F.).**
- BASEMENT FLOOR AREA 785 SFT + FIRST FLOOR AREA 985 SFT + 2ND FLOOR AREA 785 SFT.
 - TOTAL AREA 2,555 SFT.

SCALE: AS SHOWN

SIGN & STAMP.

PREPARED BY.

DESCRIPTION.

APPLICANT / OWNER.

ADDRESS.

CONCEPTUAL HOUSE DRAWINGS

DATE.
JUNE.-04-2026

PROJECT NUM.


SHEET NO.

A0.1

OF 03 Sheets (s)

CONCEPTUAL HOUSE PLANS

WITH BASEMENT

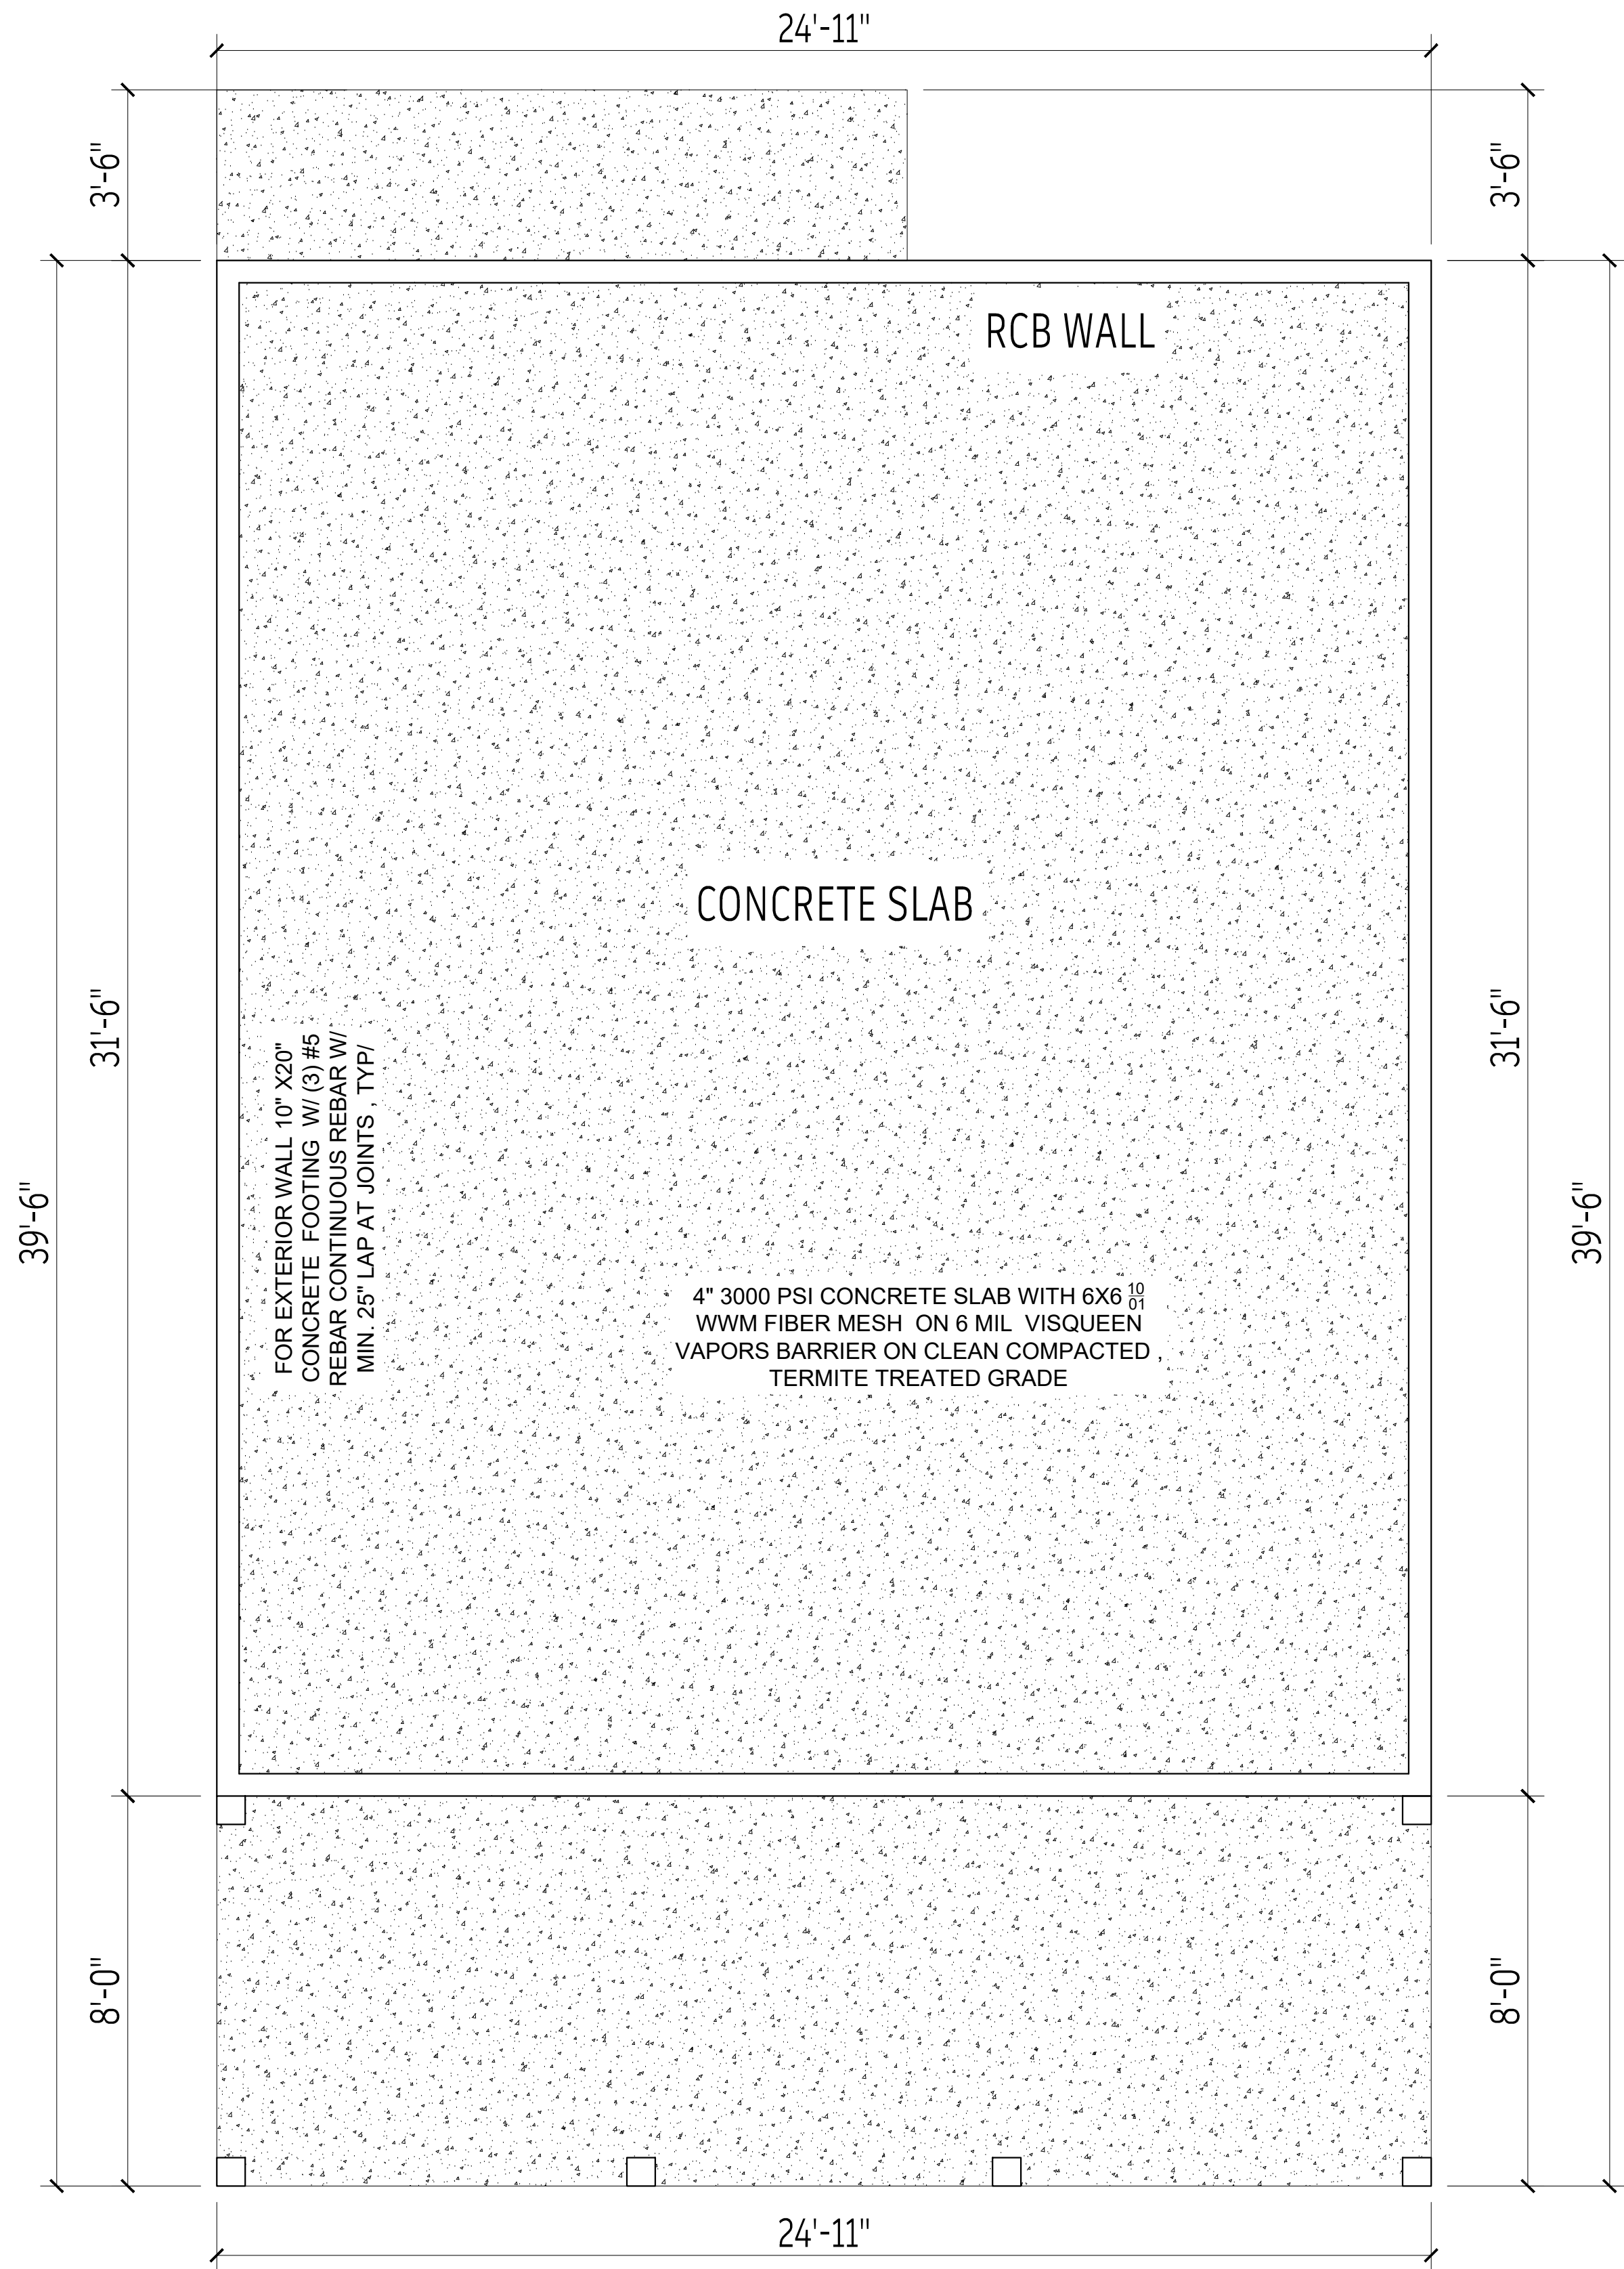

1 CONCRETE SLAB FOUNDATION.

Scale: 3/8" = 1'.0"

SCALE: AS SHOWN

SIGN & STAMP .

PREPARED BY.

DESCRIPTION .

APPLICANT / OWNER.

ADDRESS.

CONCEPTUAL HOUSE DRAWINGS

DATE.
JUNE.-04-2026





PROJECT NUM.

SHEET NO.

A0.2

OF 03 Sheets (s)

CONCEPTUAL HOUSE ELEVATIONS WITH BASEMENT

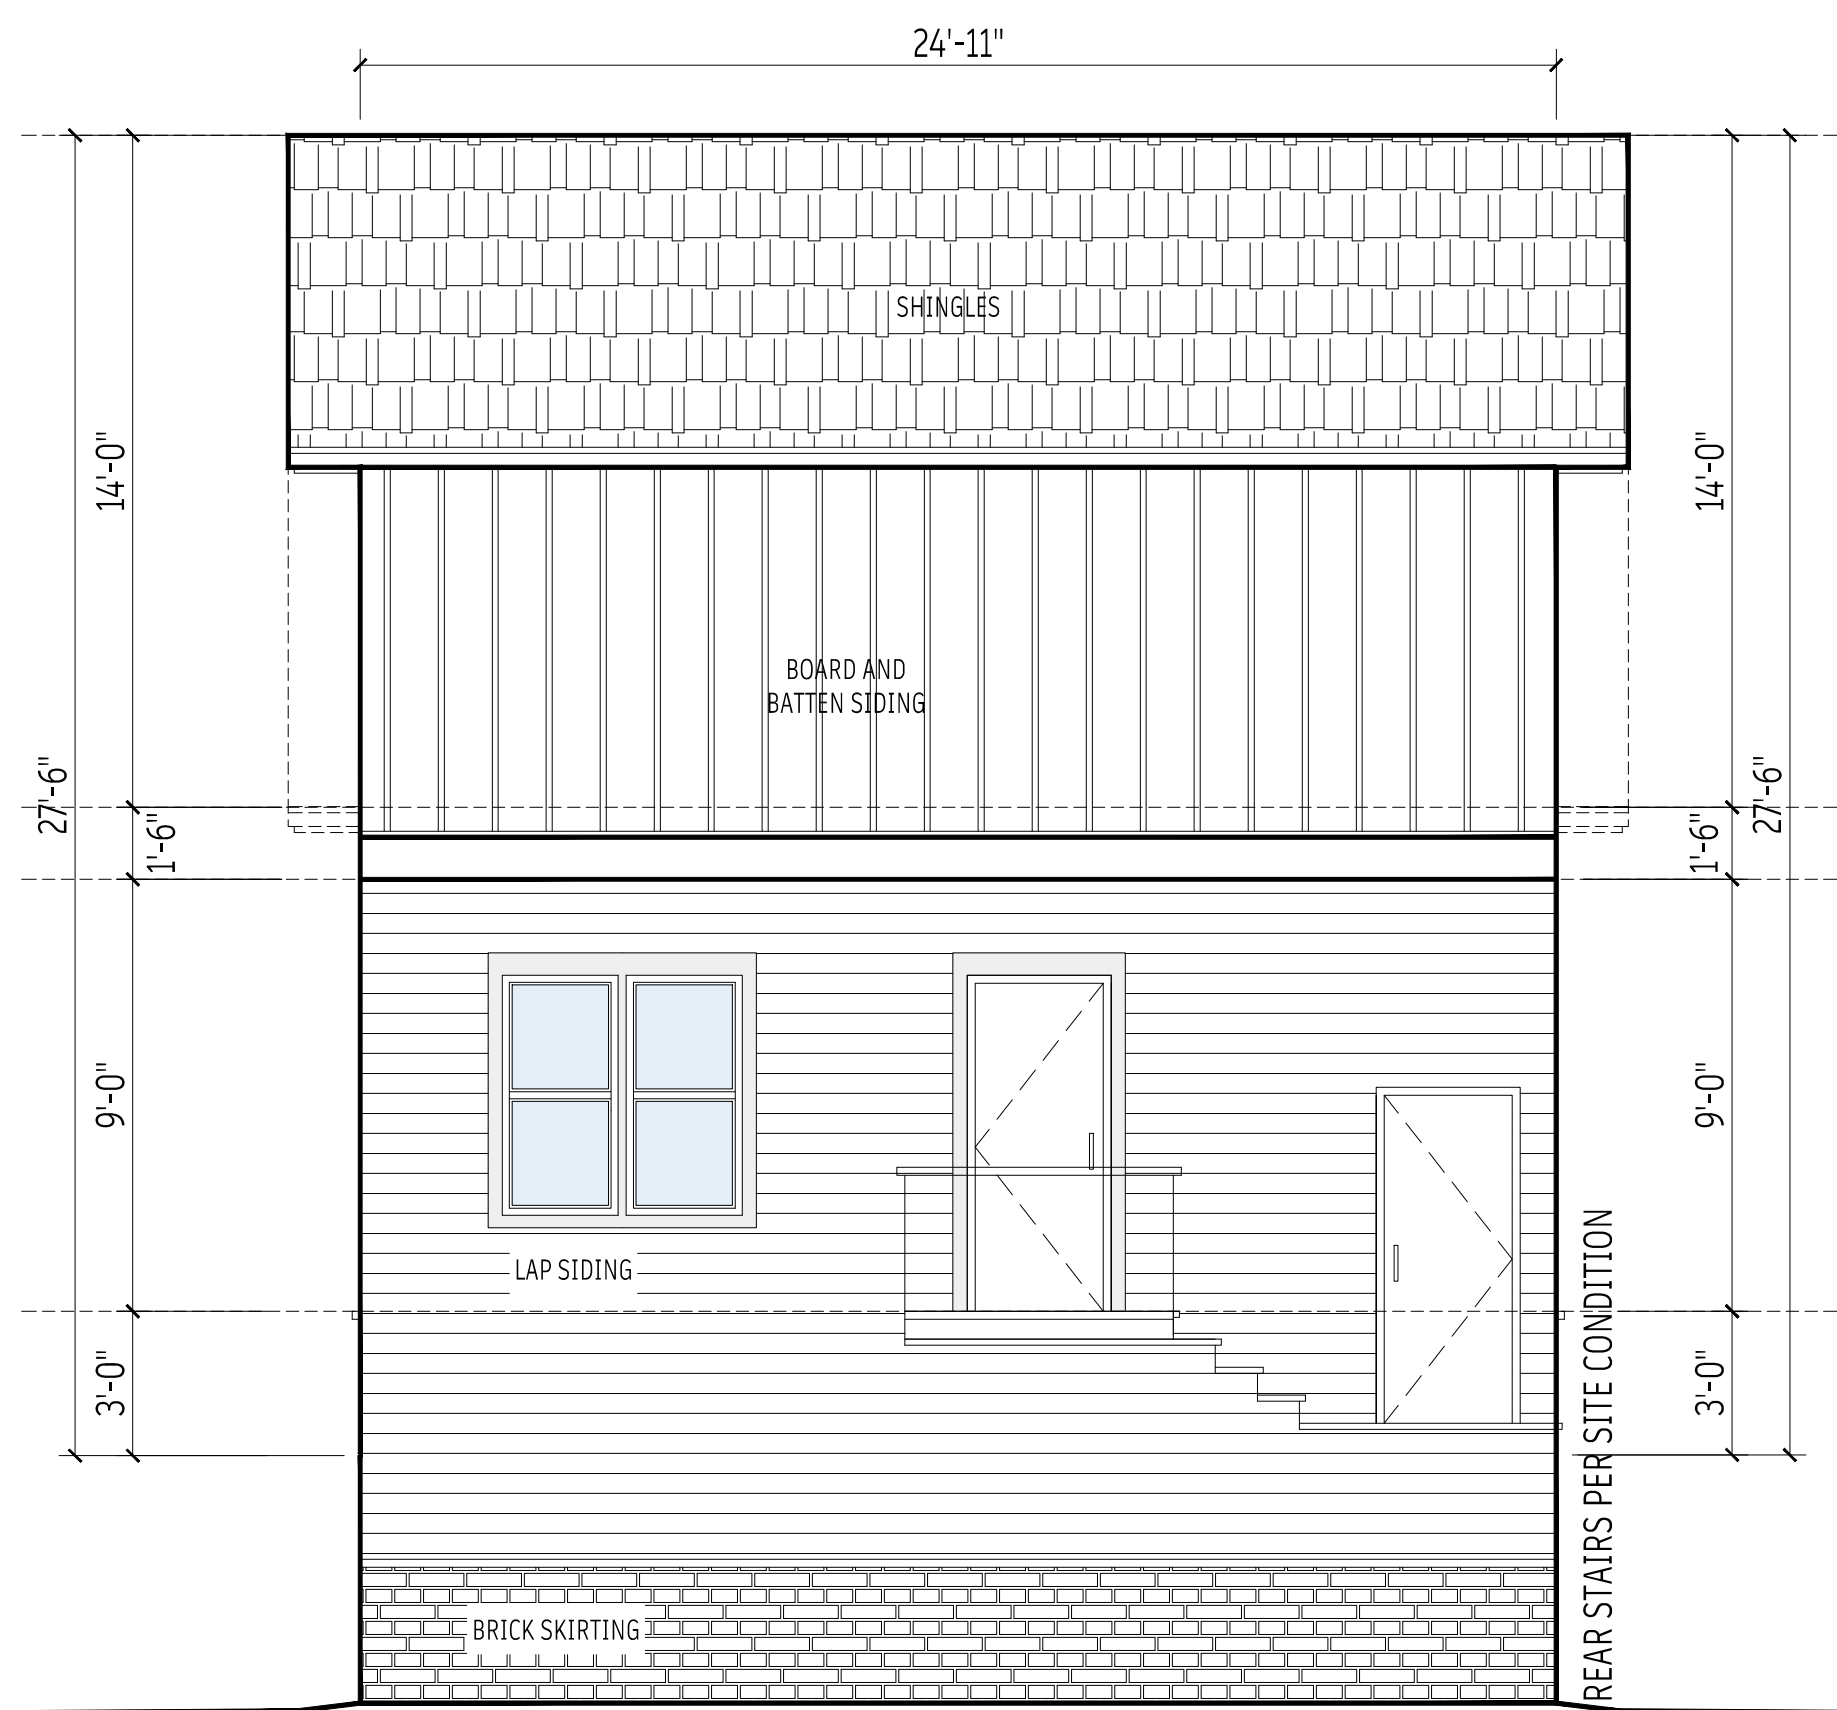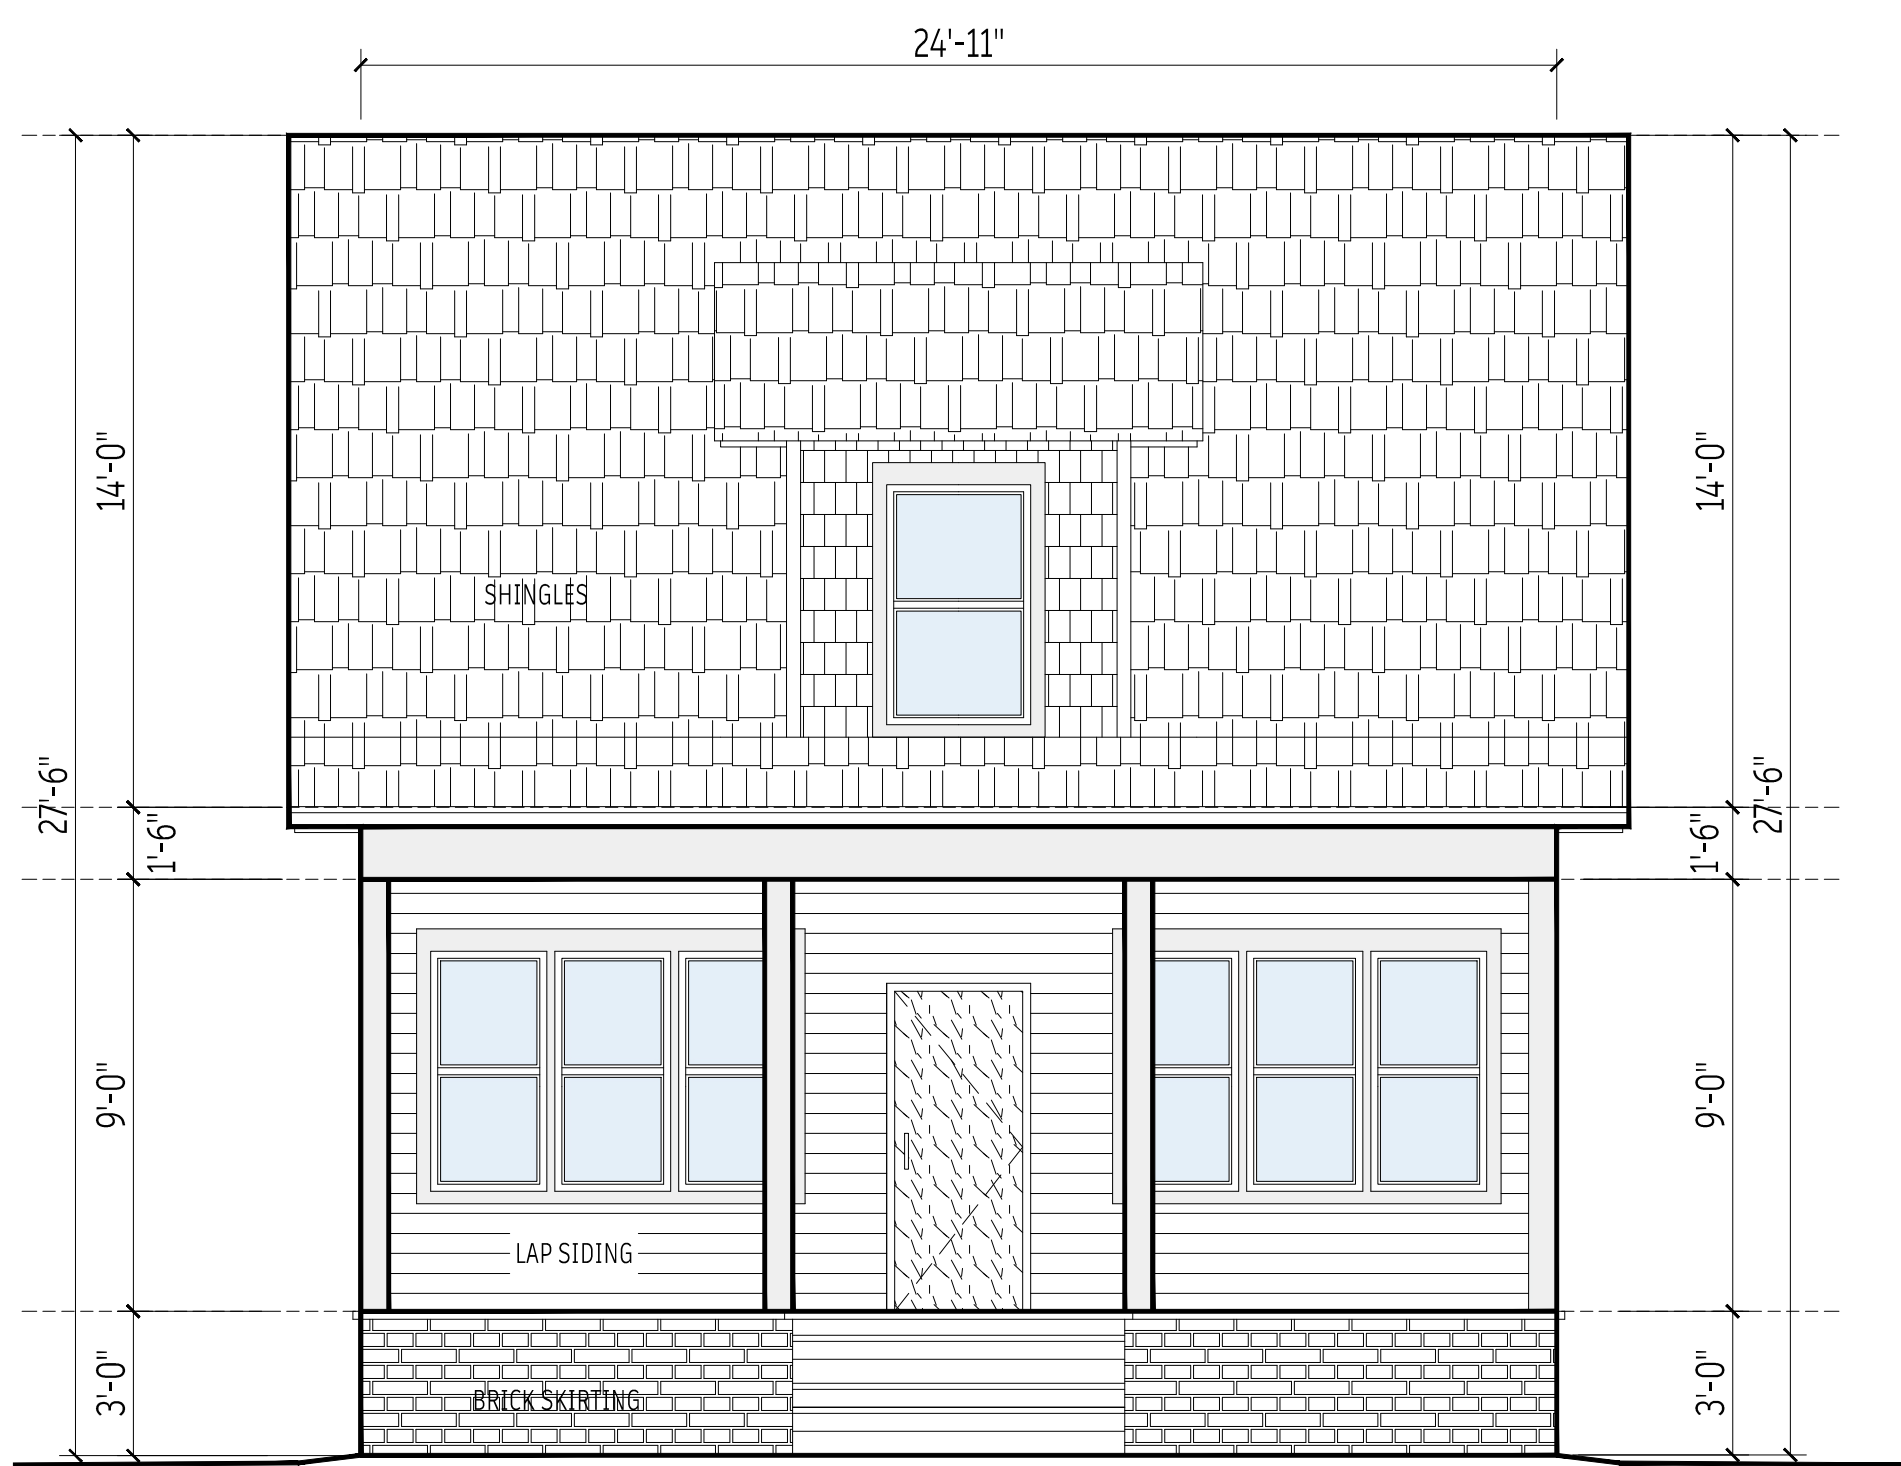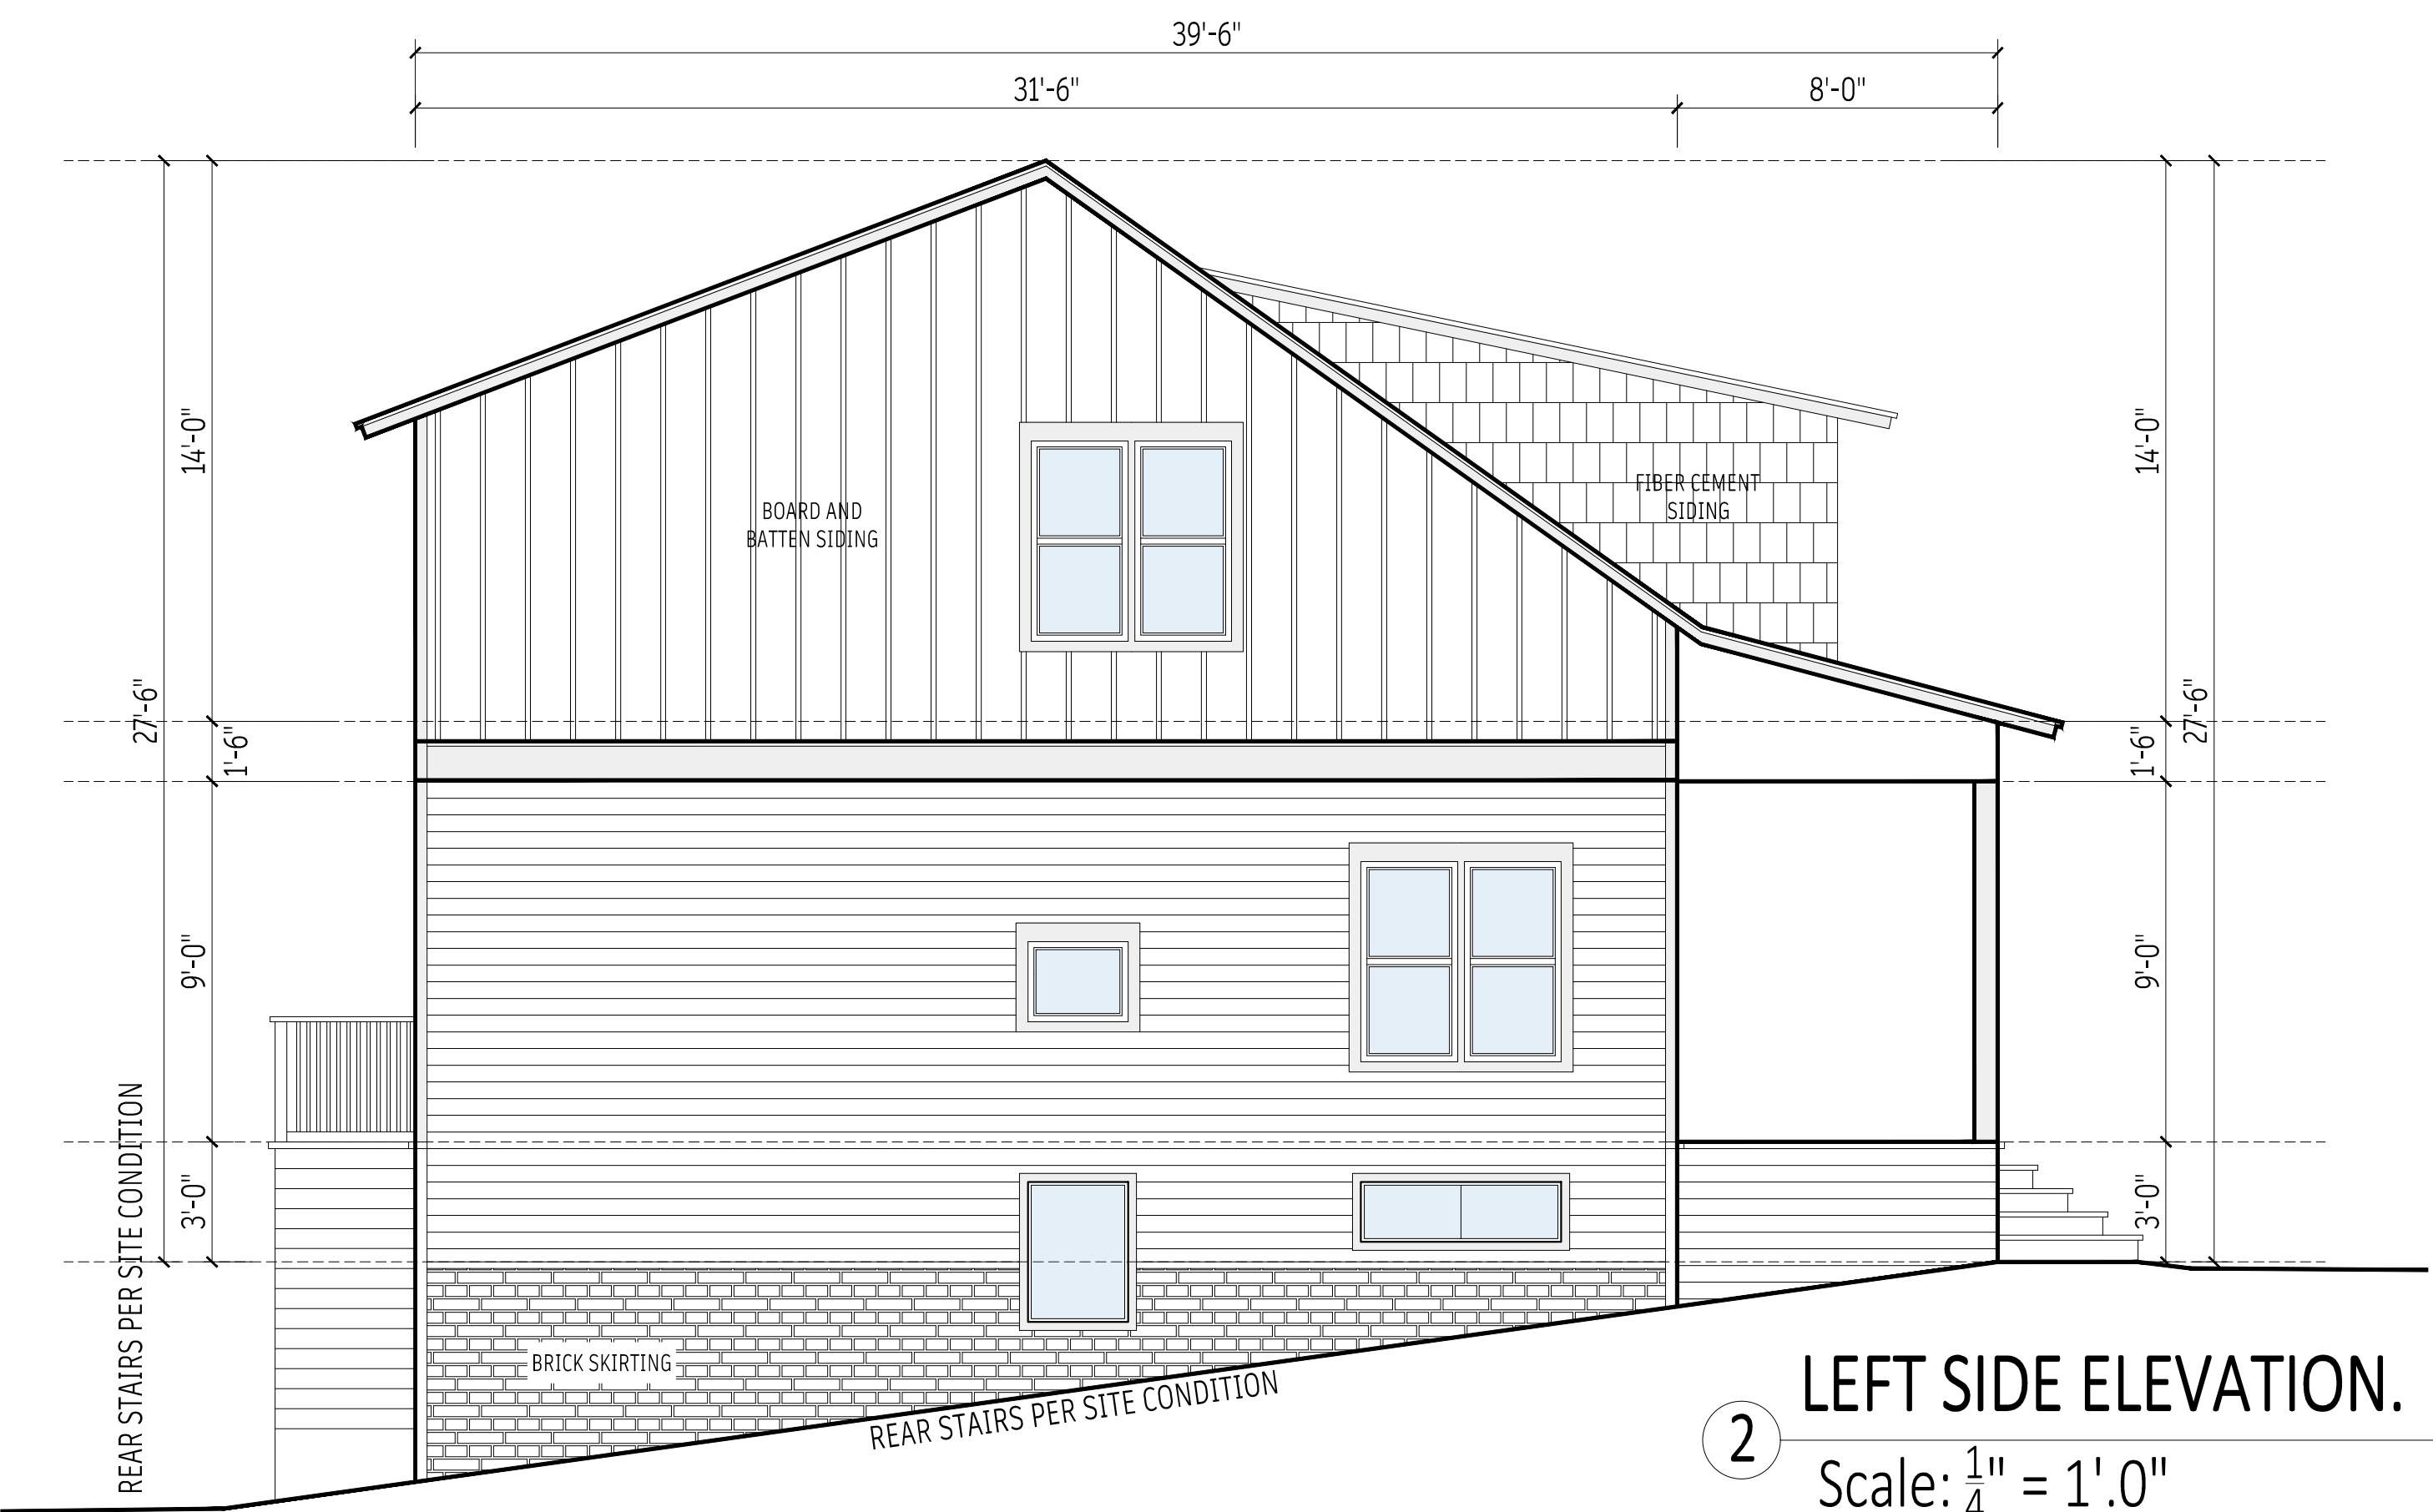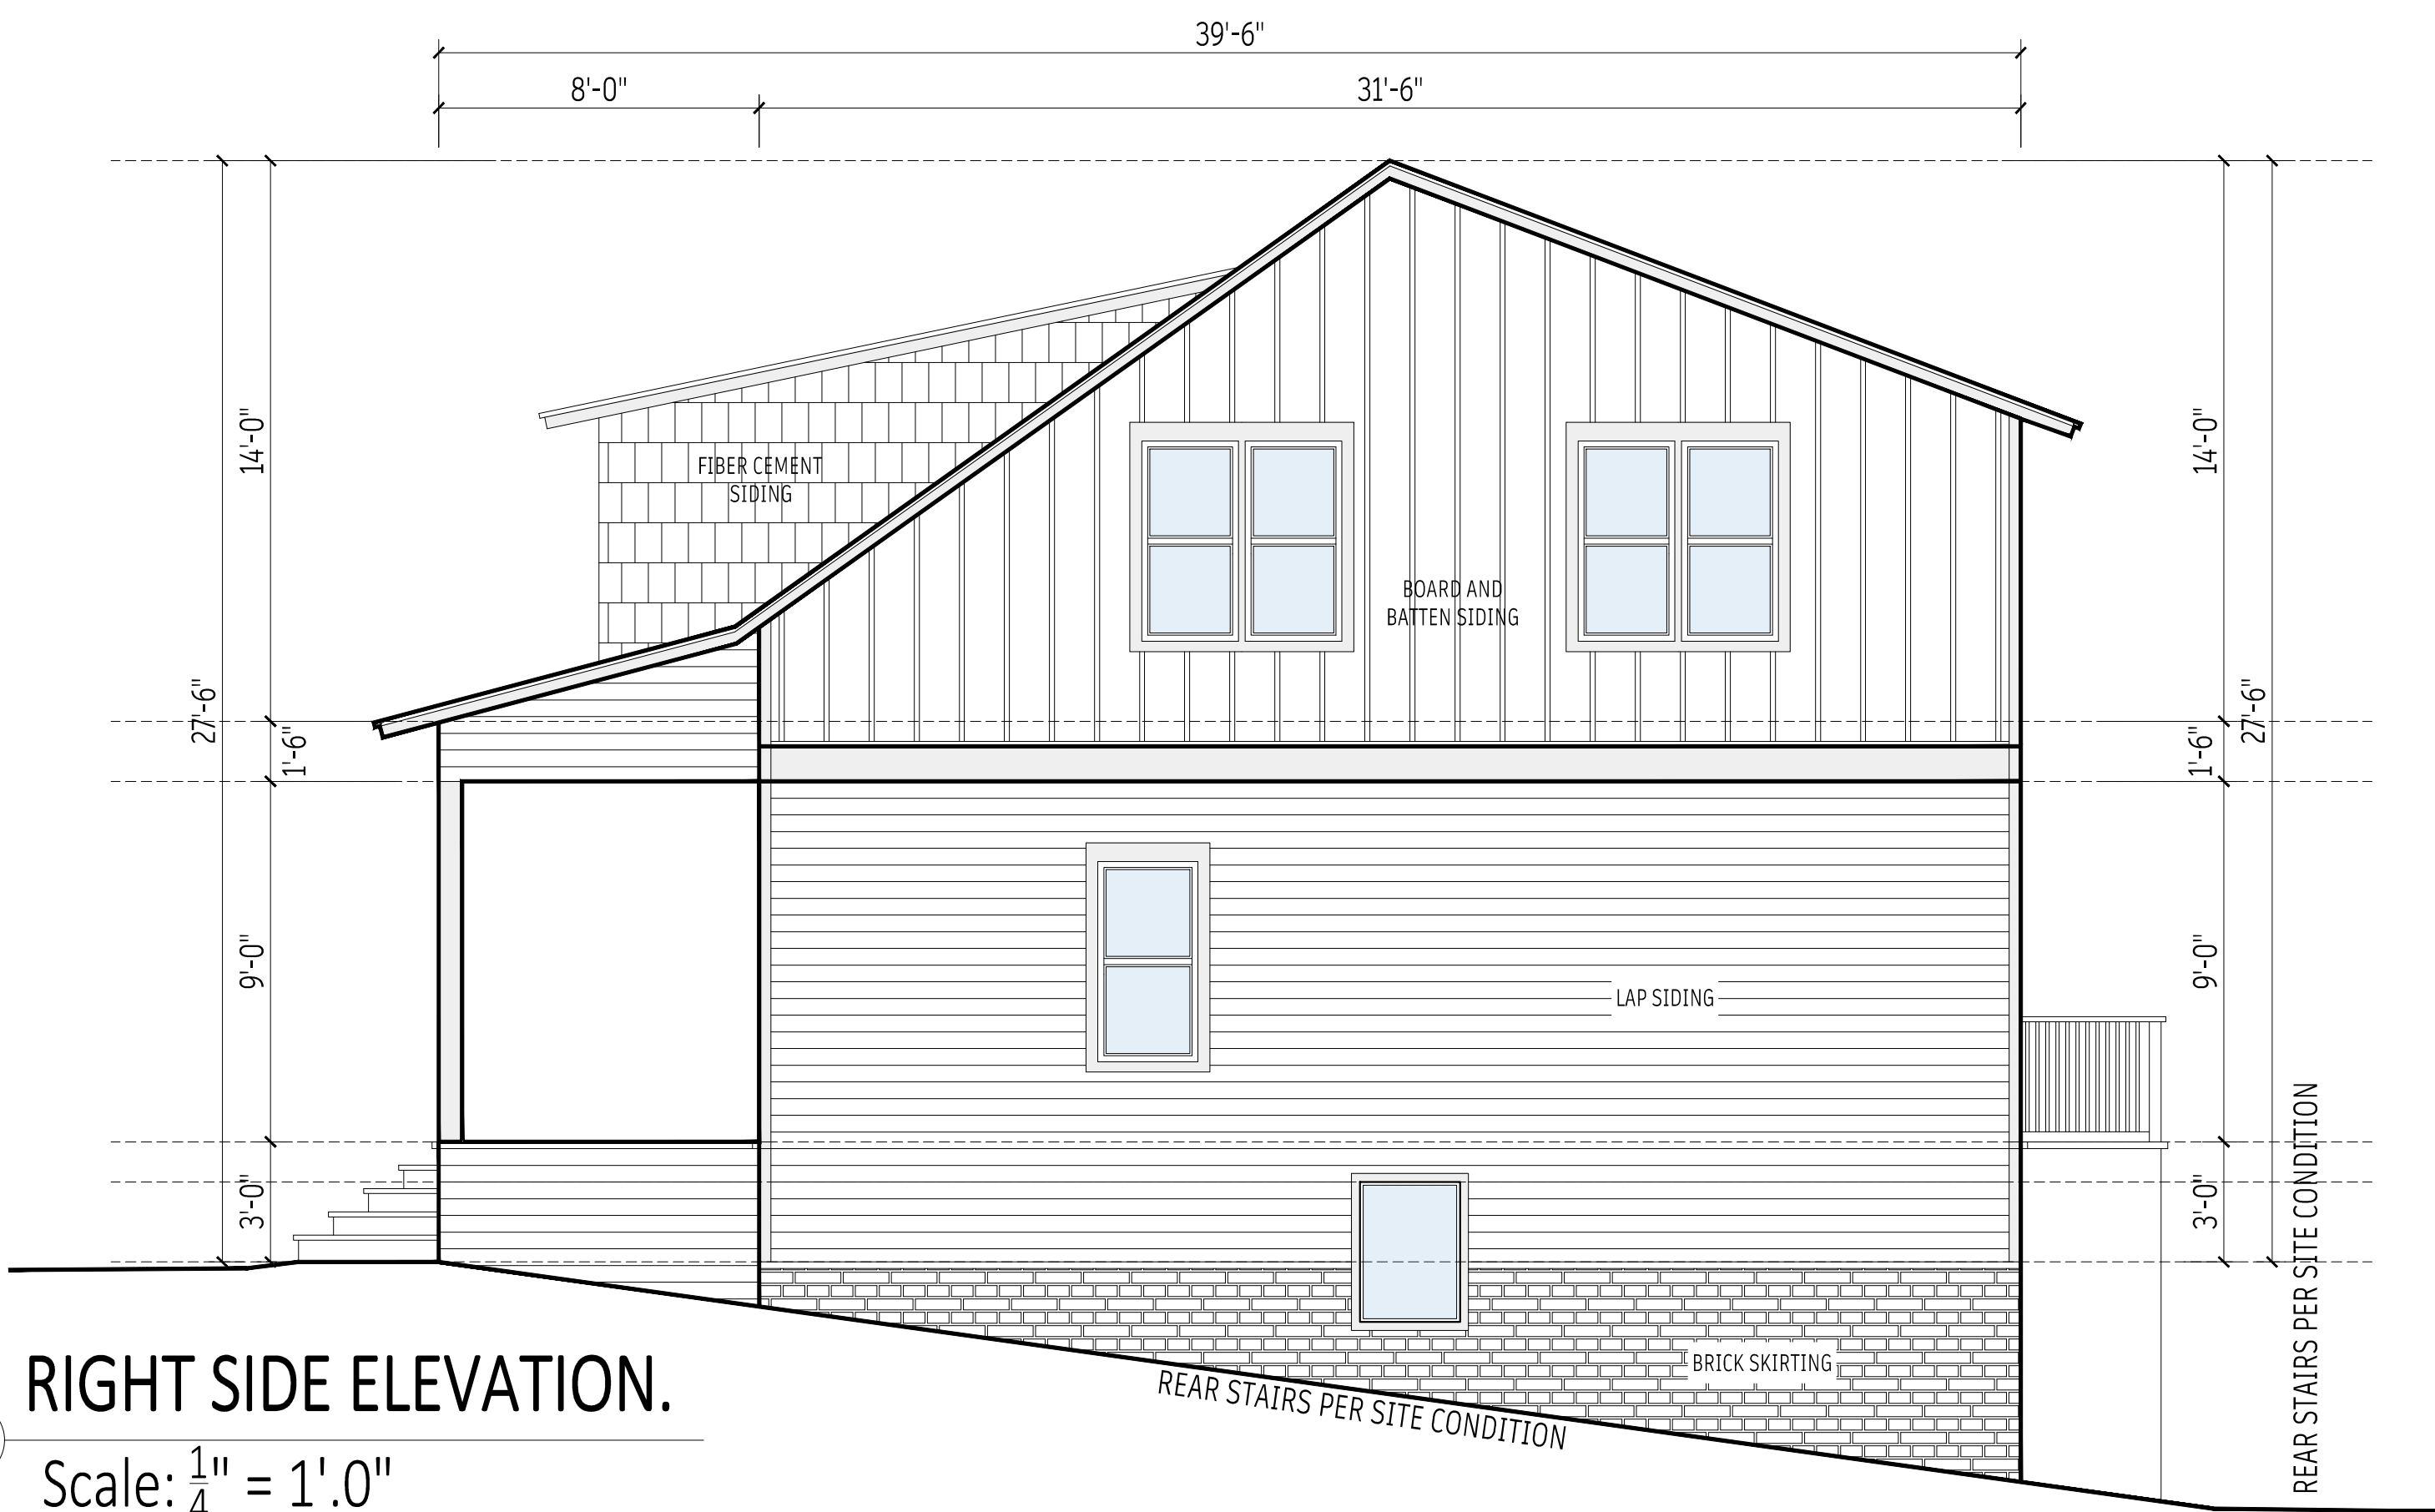

- EXTERIOR FINISHING**
1. BOARD & BATTENS.
 2. LAP SIDING
 3. BRICK SKIRTING
 4. FIBER CEMENT SIDING
 5. ROOF SHINGLES

SCALE: AS SHOWN

SIGN & STAMP .

PREPARED BY .

DESCRIPTION .

APPLICANT / OWNER.

ADDRESS.

CONCEPTUAL HOUSE DRAWINGS

DATE.
JUNE.-04-2026

PROJECT NUM.
SHEET NO.
A0.3
OF 03 Sheets (s)