




CONCEPTUAL HOUSE PLAN WITH BASEMENT

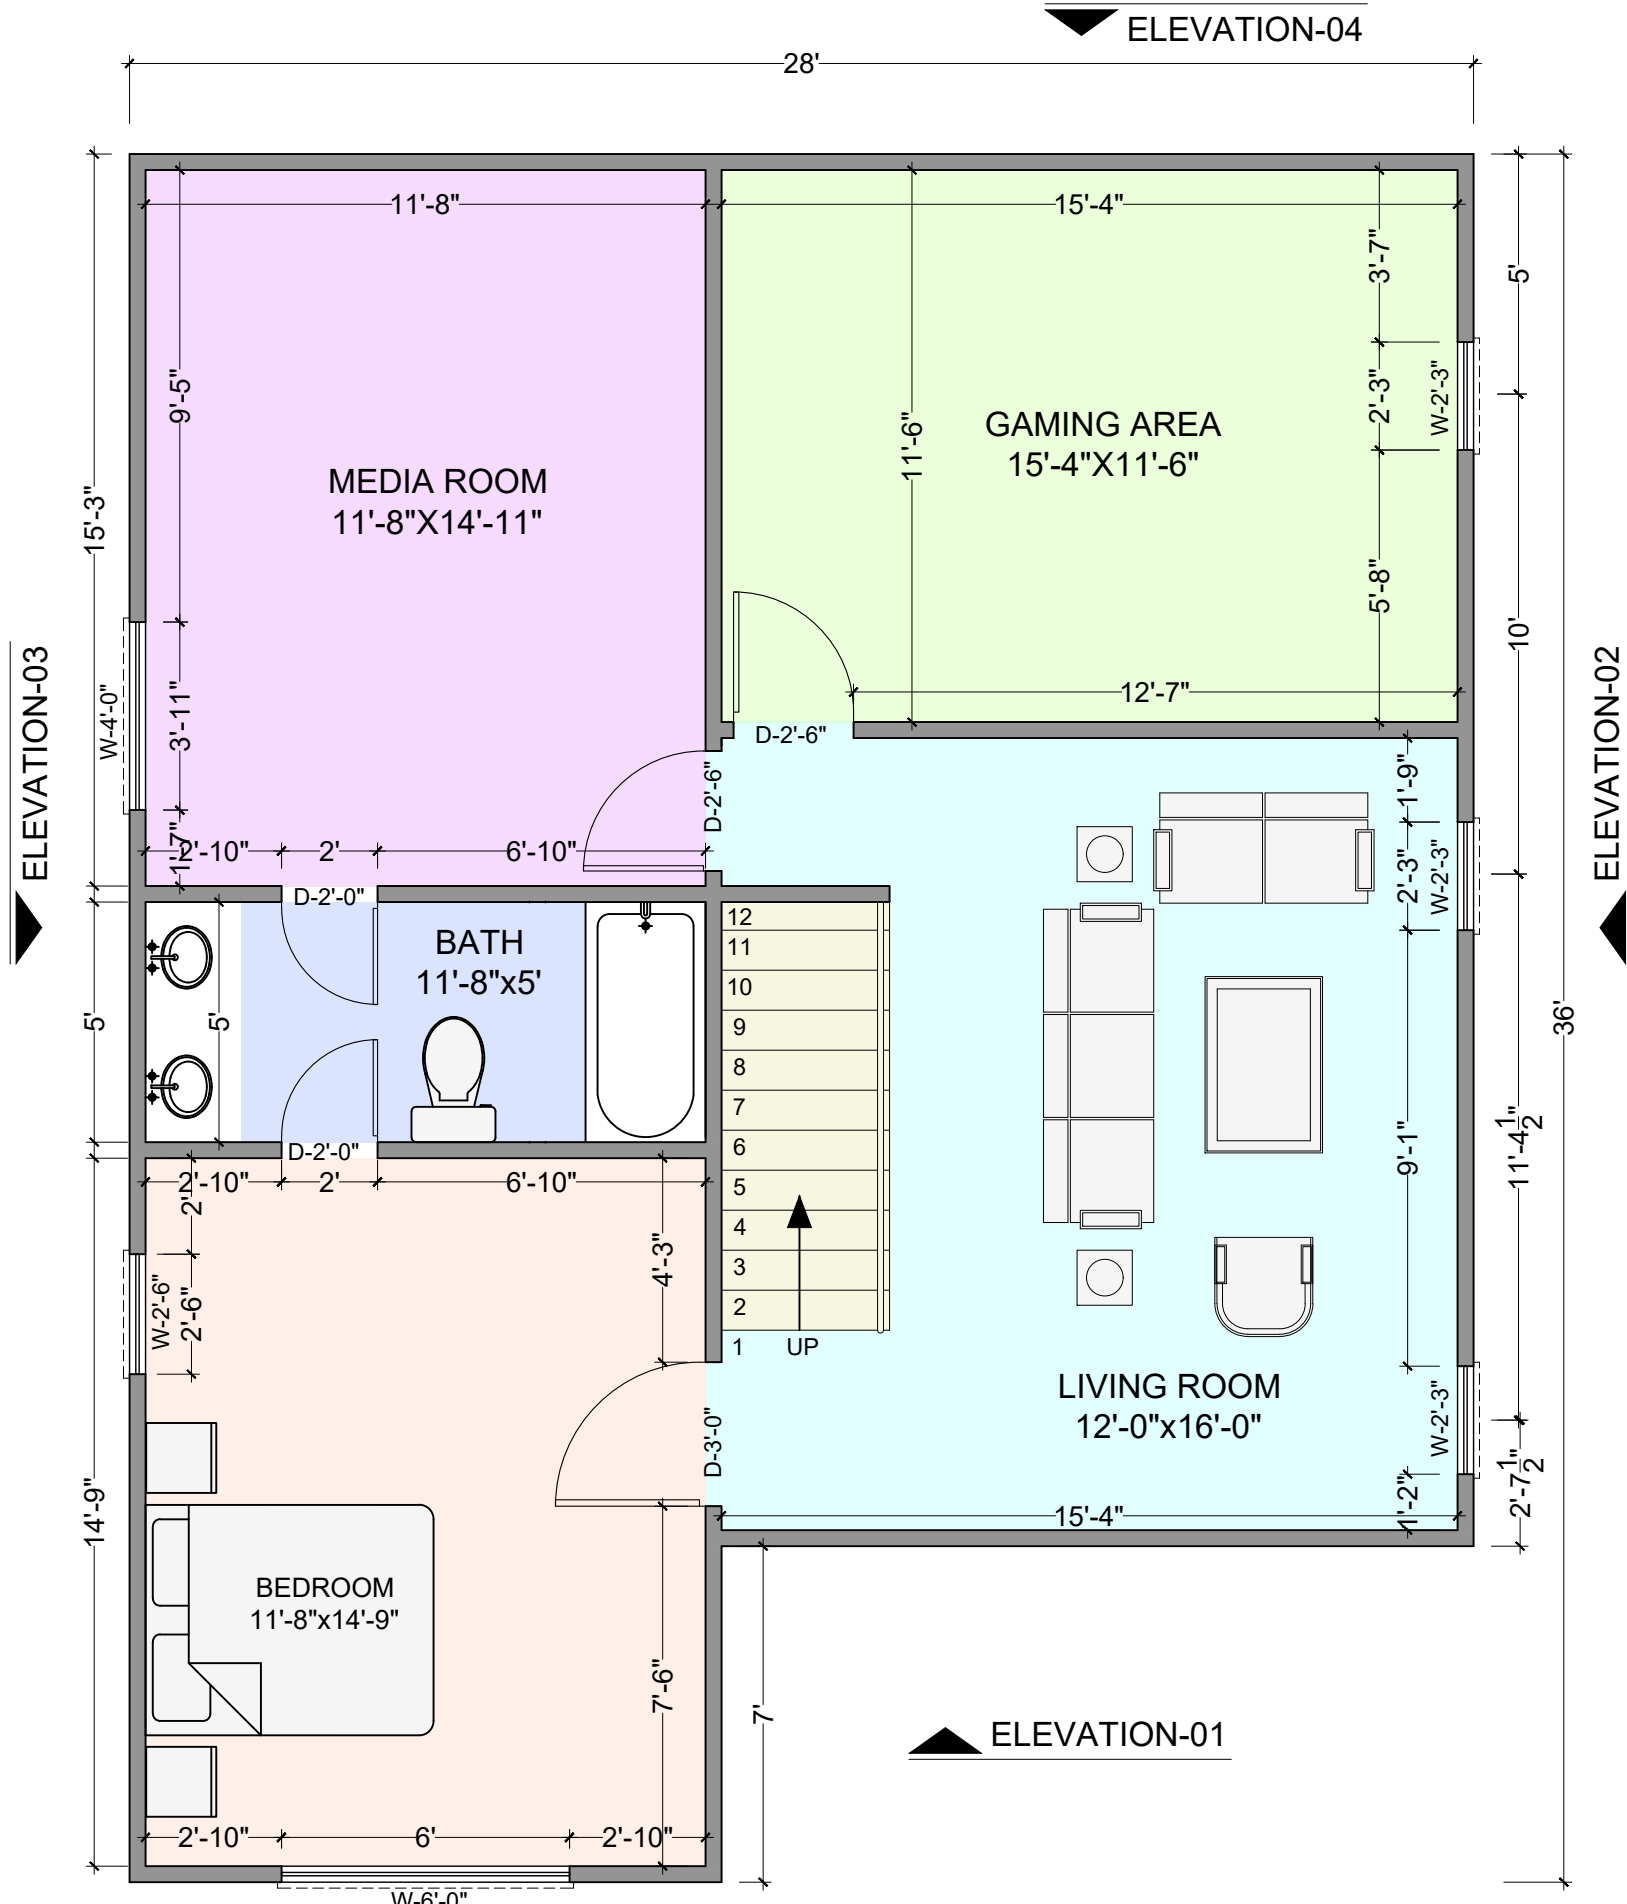

BASEMENT FLOOR PLAN
SCALE: 1/4" = 1'-0"

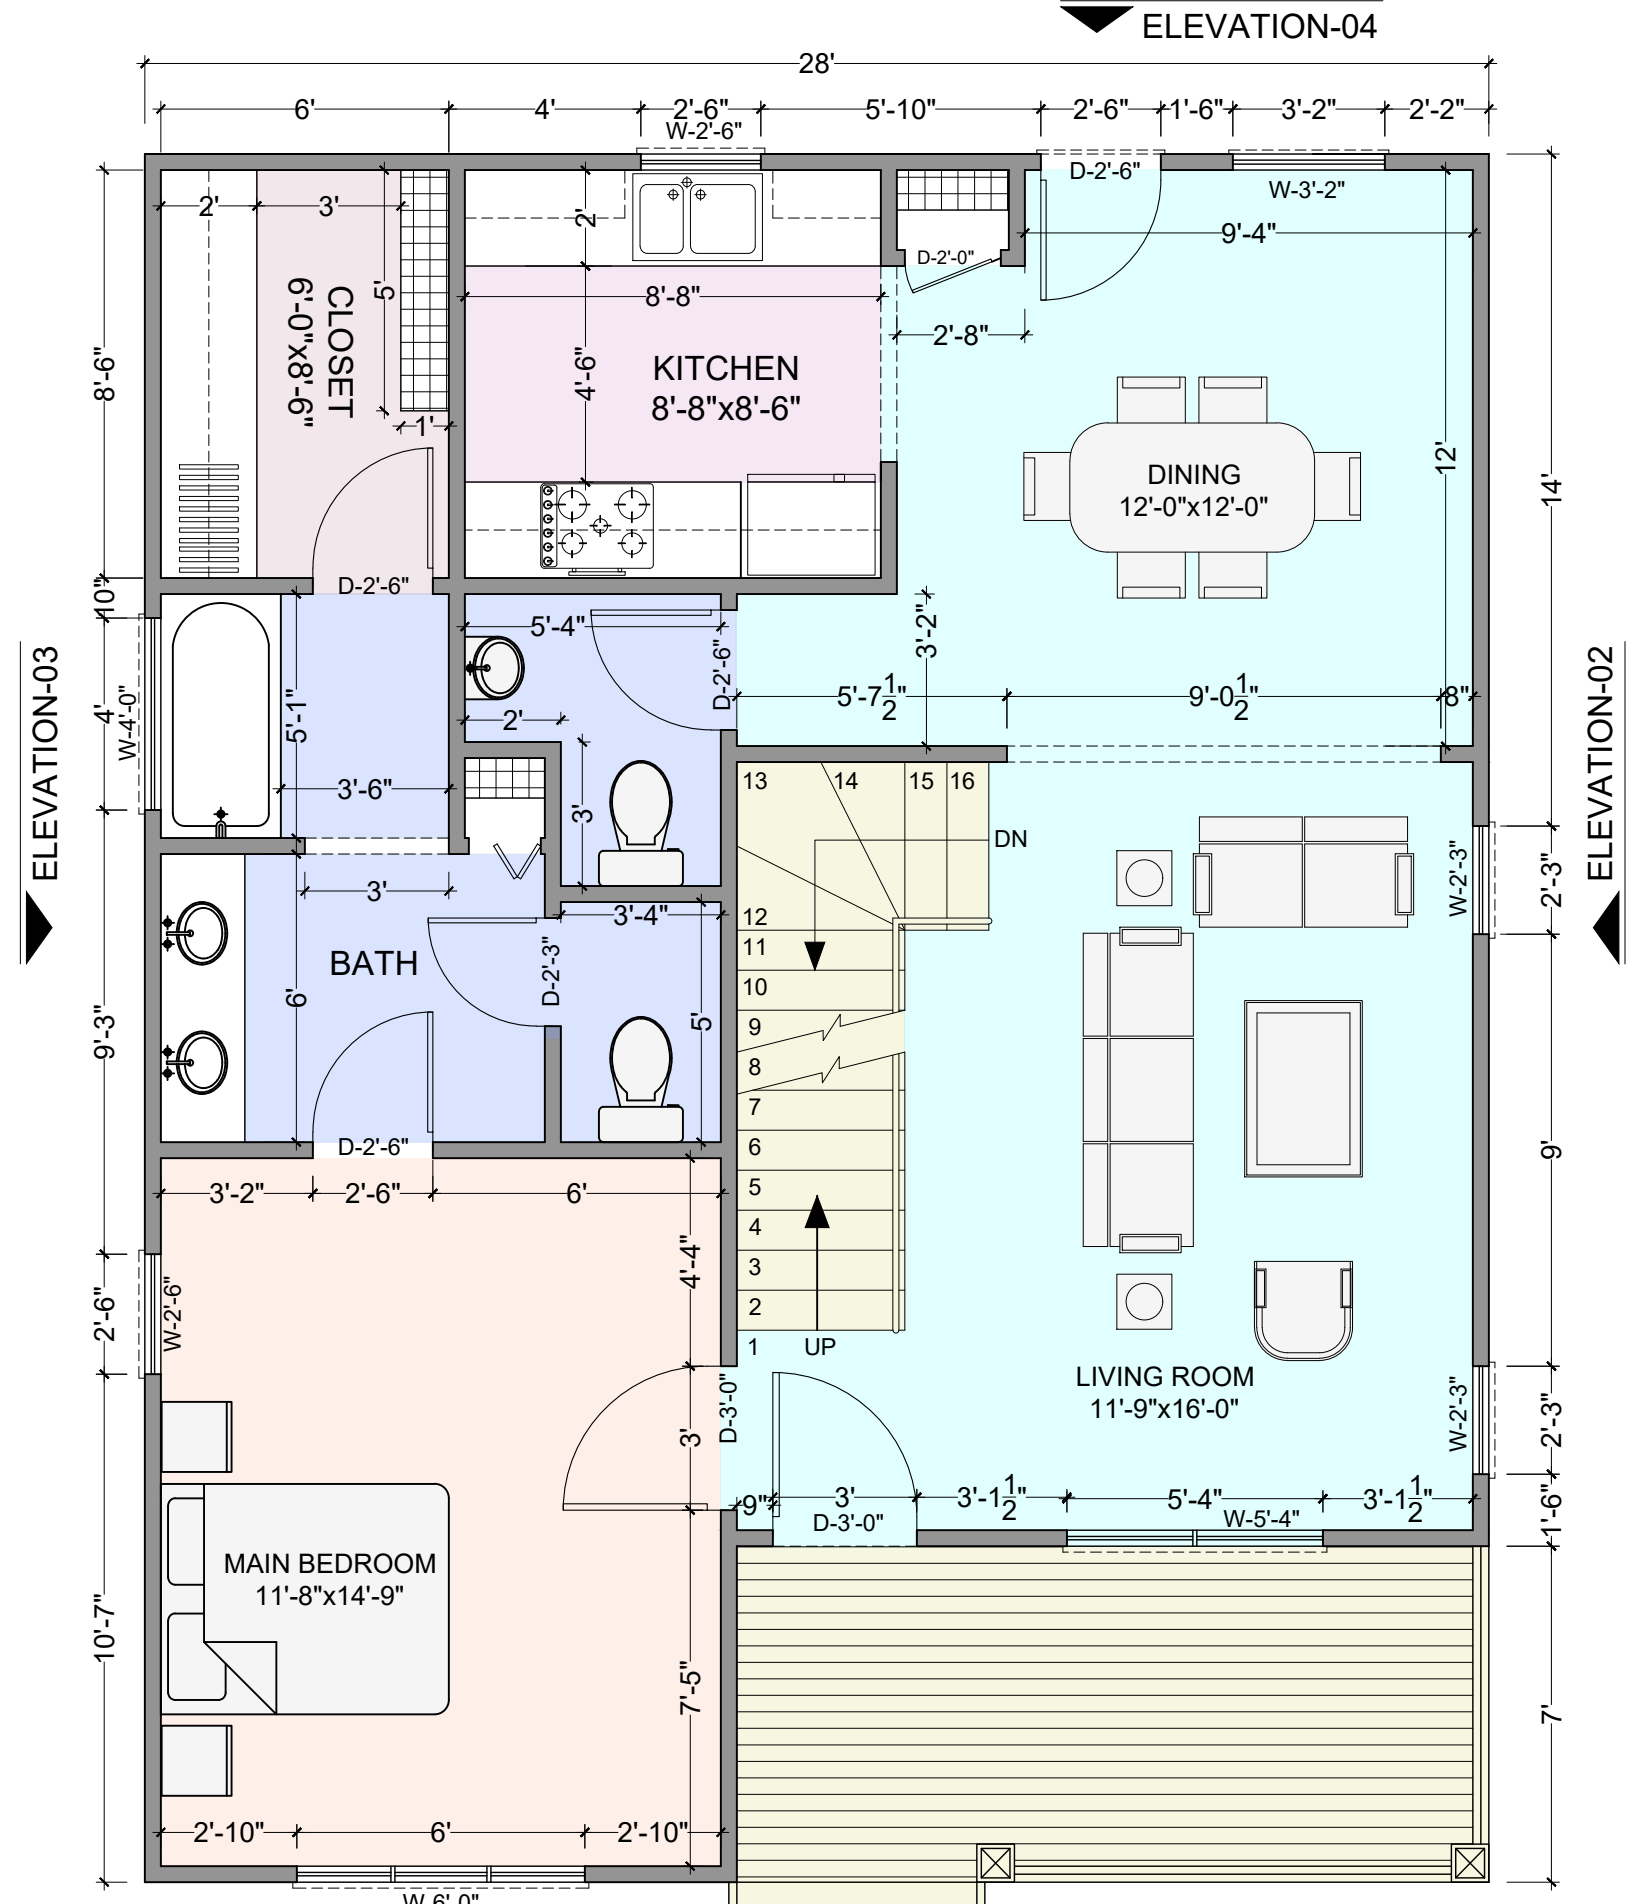

FIRST FLOOR PLAN
SCALE: 1/4" = 1'-0"

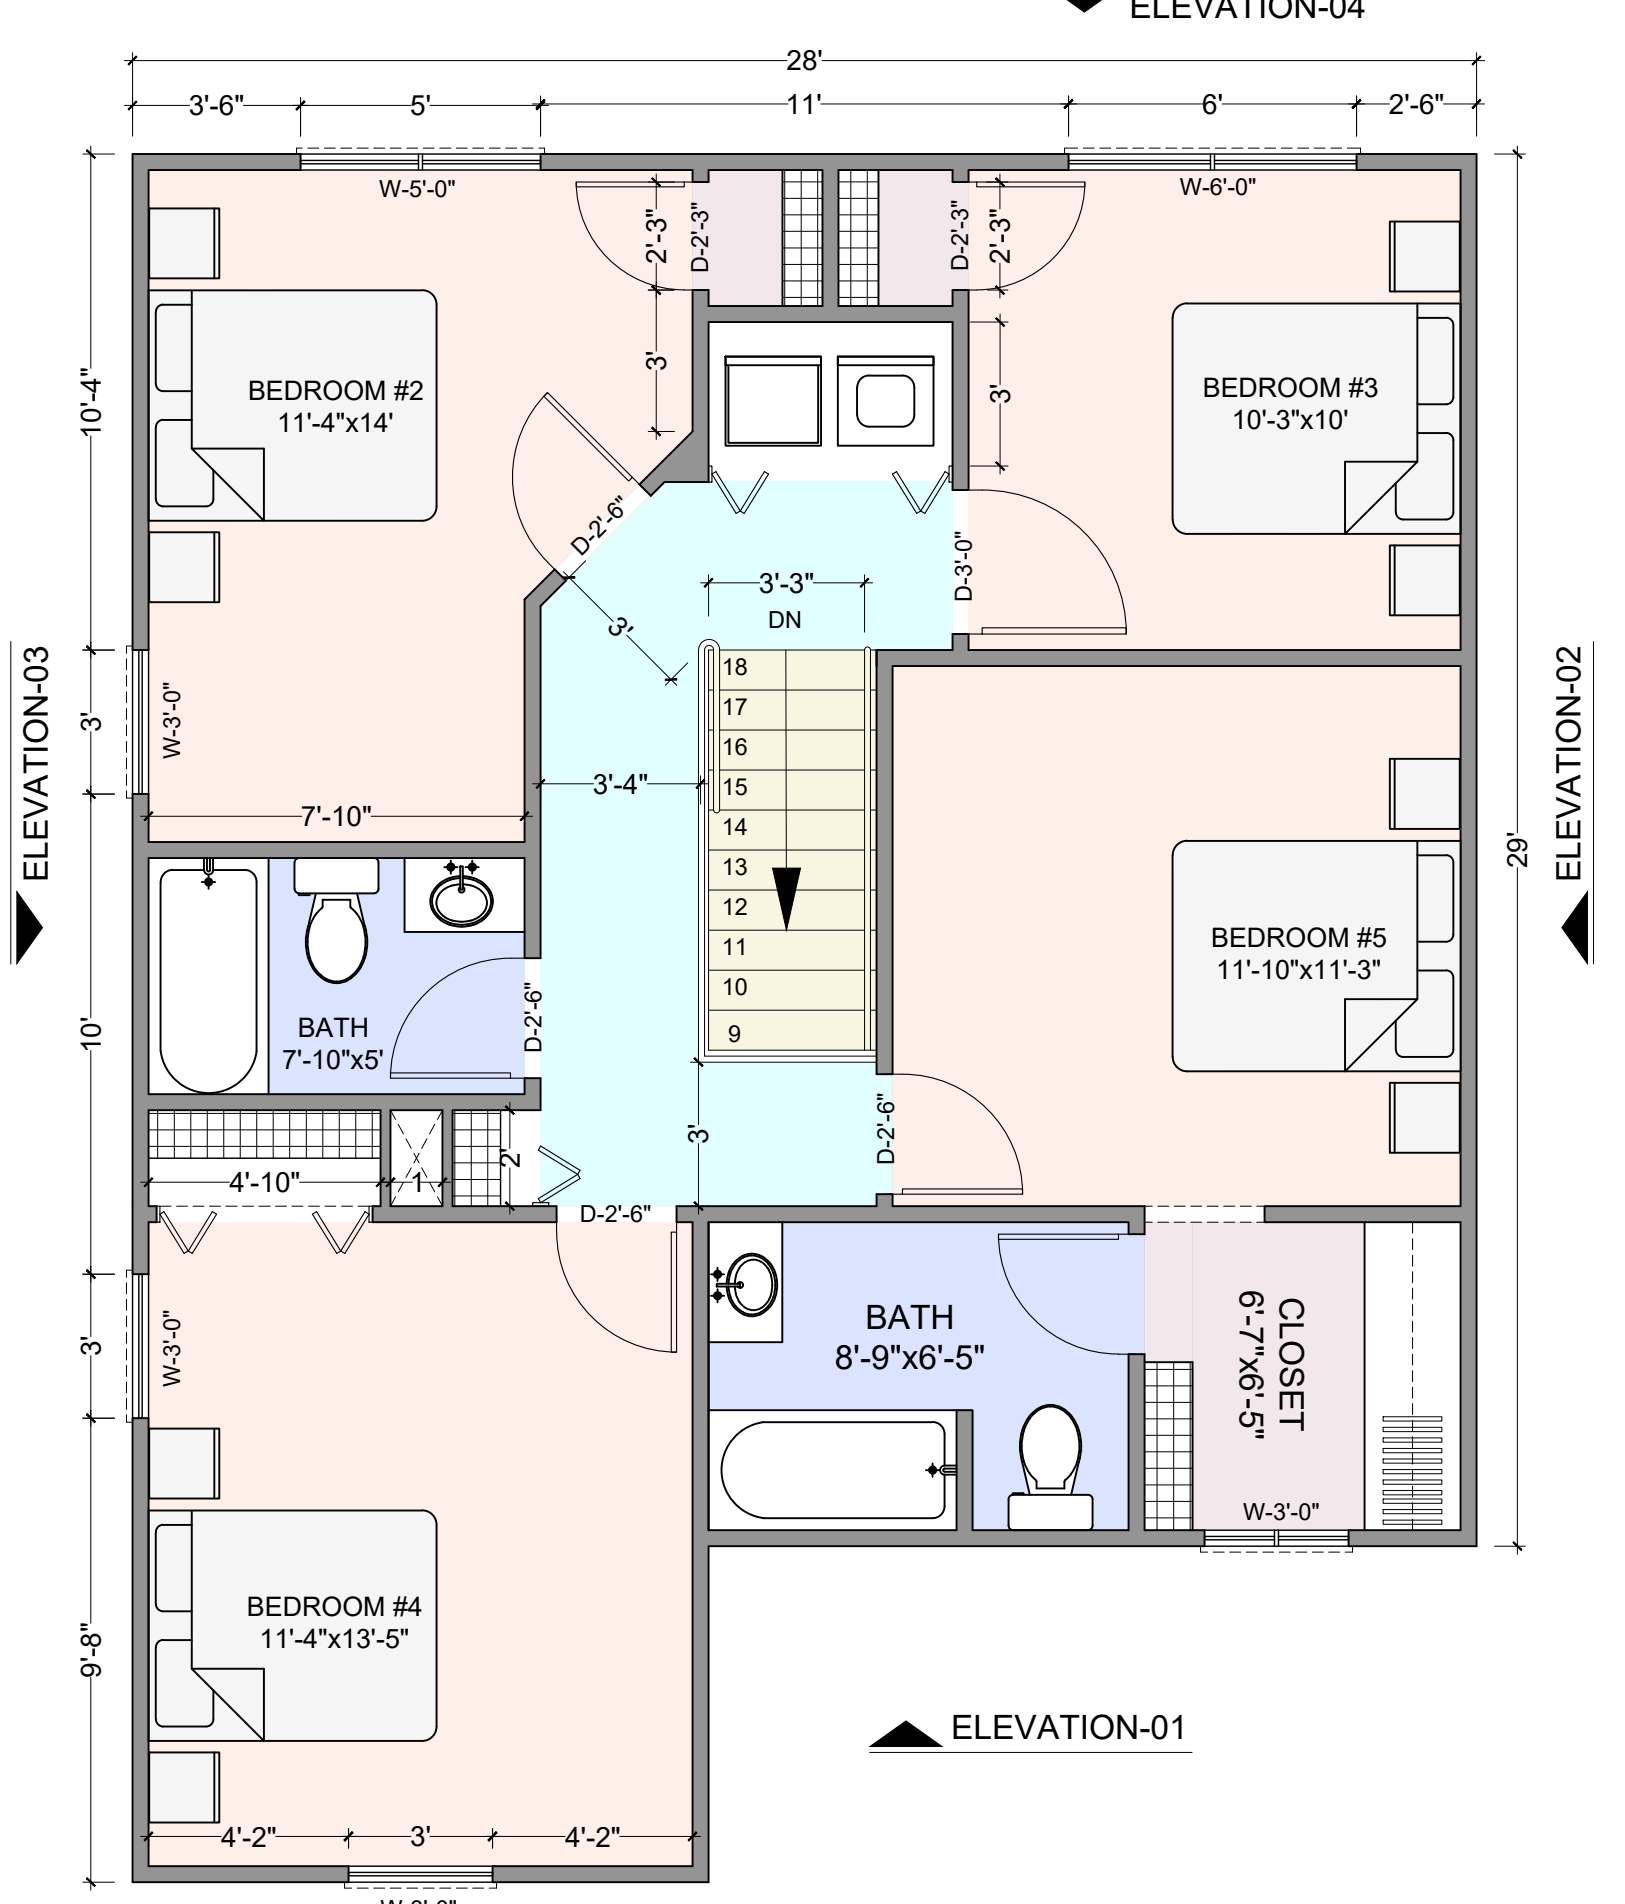

SECOND FLOOR PLAN
SCALE: 1/4" = 1'-0"

NOTE:
1. ALL DIMENSIONS ON THIS DRAWING SHALL BE CHECKED ON SITE BEFORE WORK COMMENCES.
2. FIGURED DIMENSIONS SHALL BE TAKEN IN PREFERENCE TO SCALE DIMENSIONS.
3. ALL DISCREPANCIES ARE TO BE REPORTED FOR CLARIFICATION BEFORE WORK COMMENCES.

REVISION NOTES		
DATE	DESCRIPTION	BY

JOB NO.
SCALE: 1/4" = 1'-0"

PREPARED BY.

DESCRIPTION .

CONCEPTUAL HOUSE PLAN

APPLICANT / OWNER.

ADDRESS. 79-299


DATE.
11-JUN-2026

SHEET NO.
A-01


EXTERIOR OPTION: COMBINED




ELEVATION-01
SCALE: 1/4" = 1'-0"

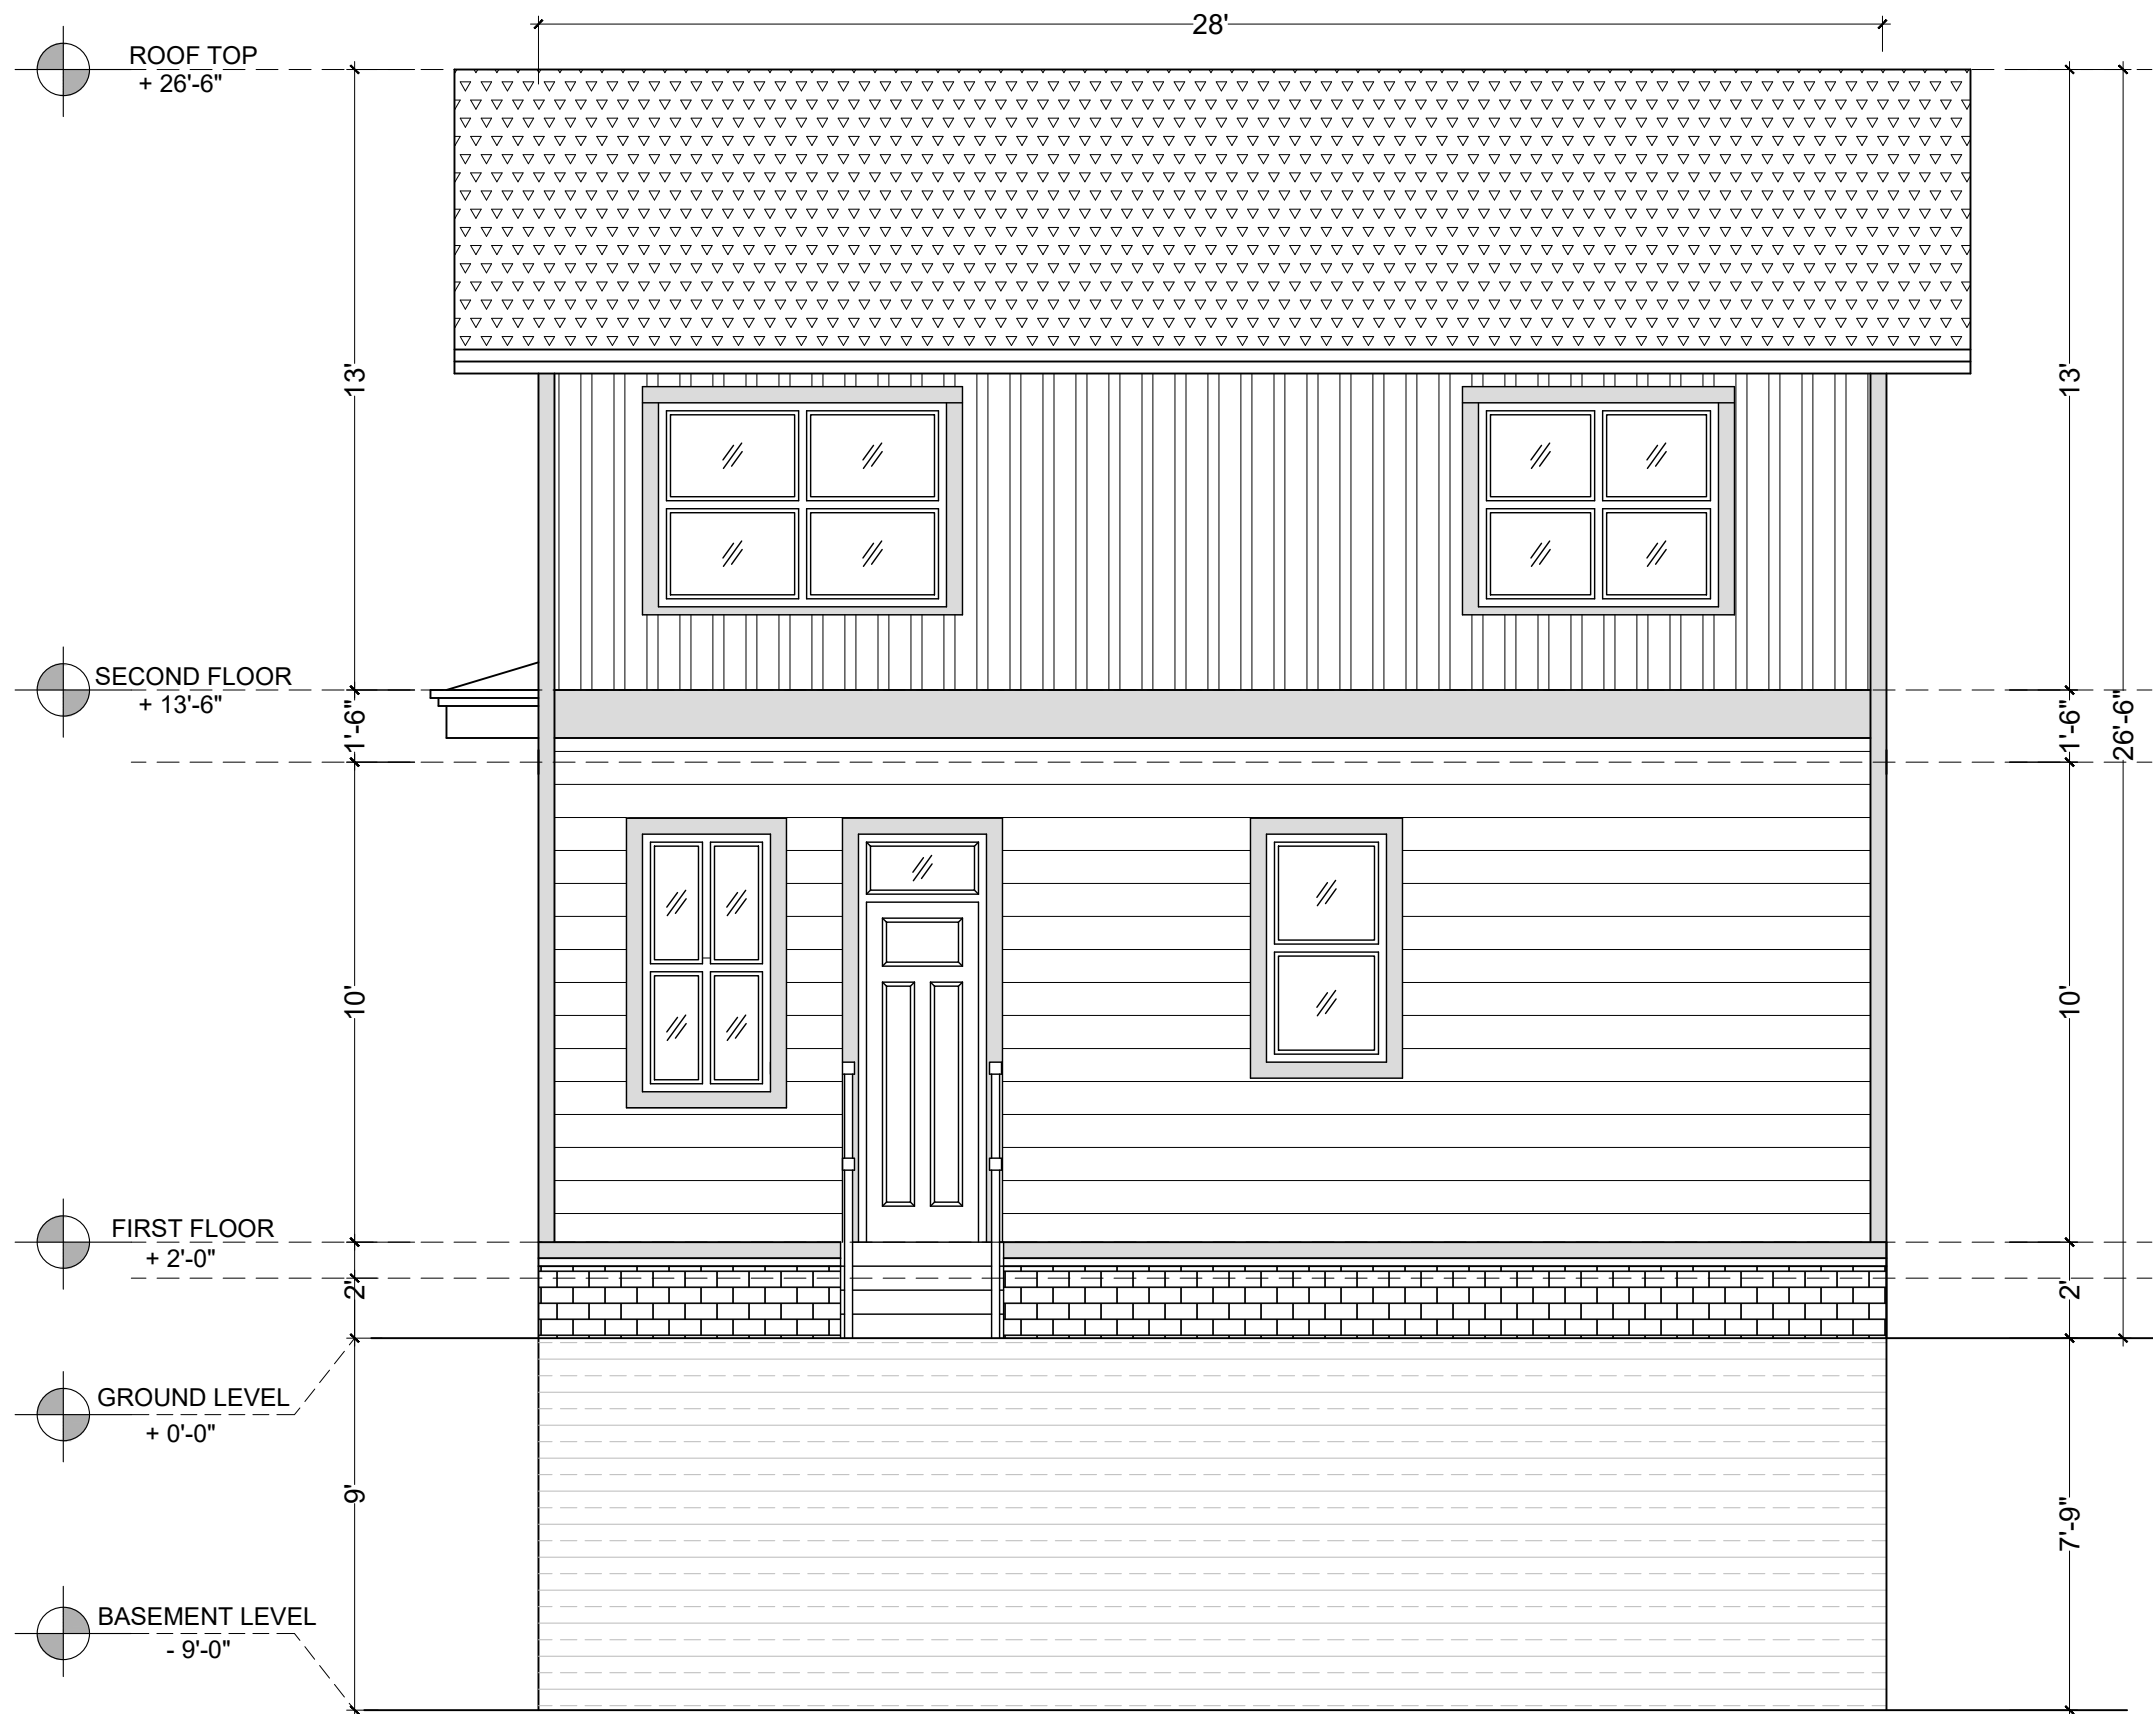

ELEVATION-04
SCALE: 1/4" = 1'-0"

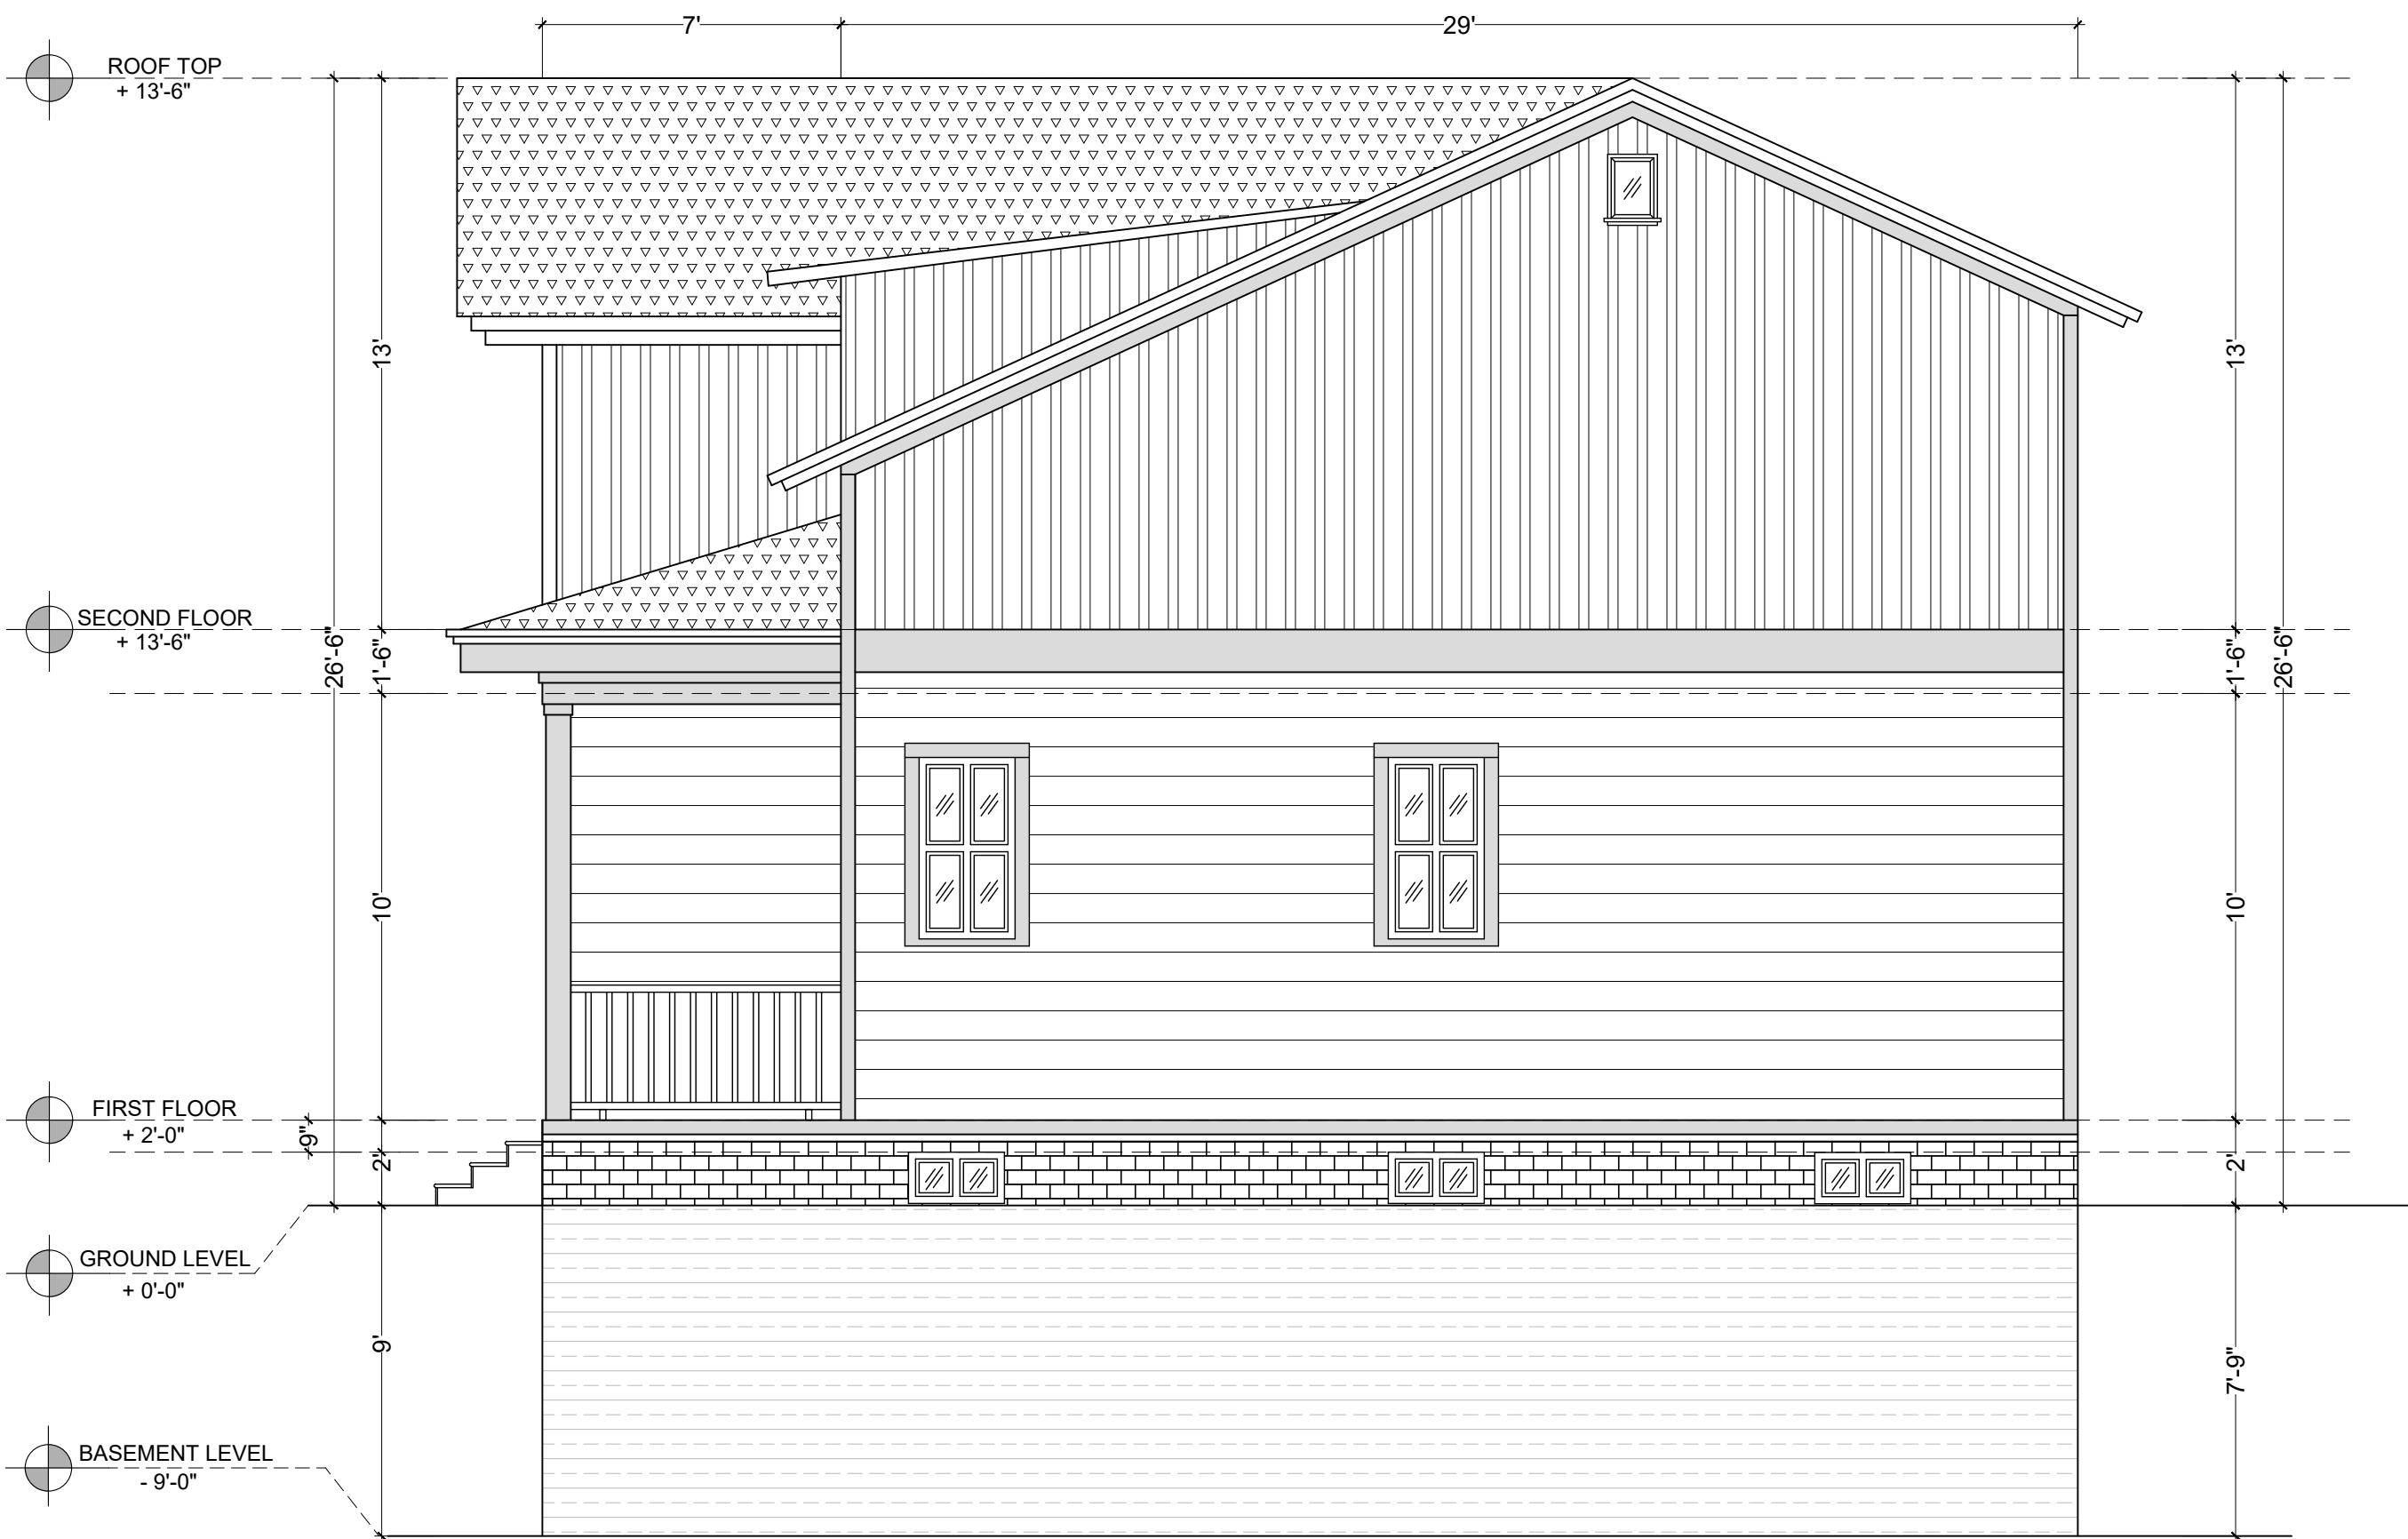

ELEVATION-02
SCALE: 1/4" = 1'-0"

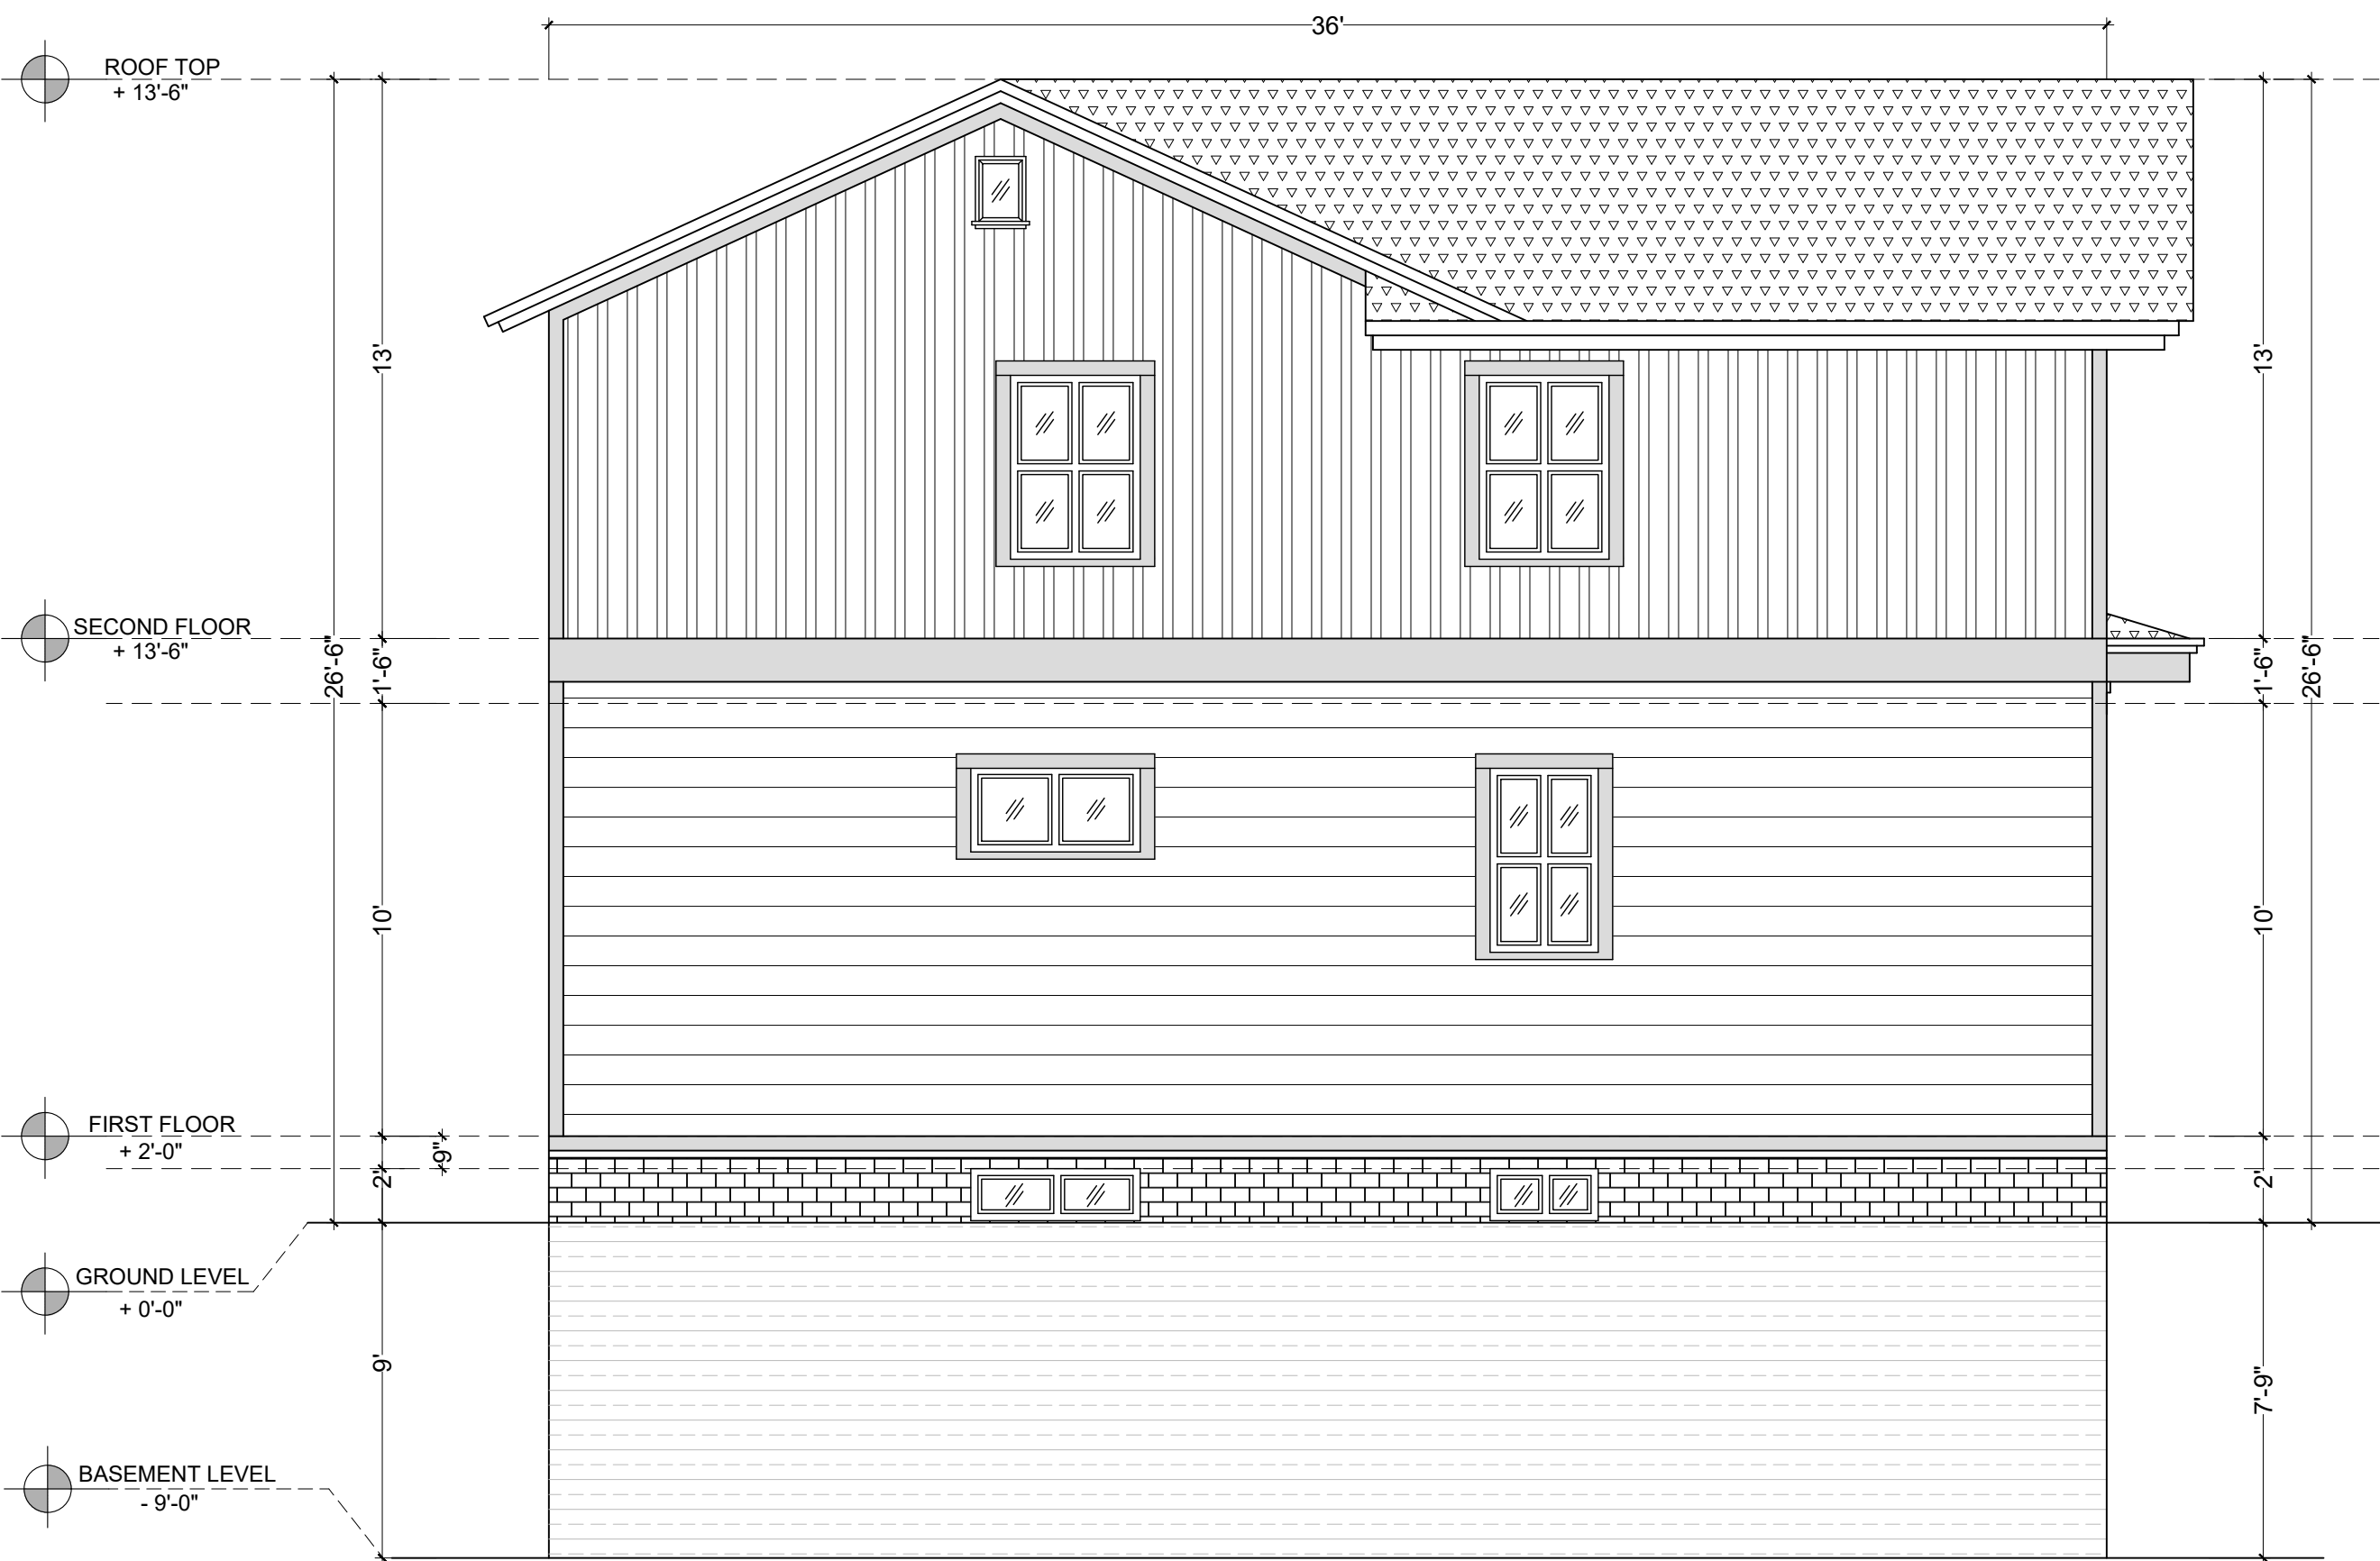

ELEVATION-03
SCALE: 1/4" = 1'-0"

COMMENTS ON COMBINED FINISHES

- PERFORMANCE**
- CAN BE HIGH-PERFORMING IF DETAILED CORRECTLY
- ALLOWS:
- BRICK = MOISTURE PROTECTION
- LAP = PRIMARY WEATHER BARRIER
- B&B = ACCENT
- DURABILITY**
- GOOD OVERALL IF:
- MATERIALS ARE COMPATIBLE
- TRANSITIONS ARE PROPERLY DETAILED
- MAINTENANCE**
- BRICK = LOW
- LAP = MODERATE
- B&B = HIGHER
- MORE MATERIALS = MORE MAINTENANCE TYPES
- COST**
- HIGHEST COST OVERALL:
- MORE MATERIALS
- MORE LABOR
- MORE DETAILING
- RISKS**
- TRANSITIONS BETWEEN MATERIALS

- NOTE:
- ALL DIMENSIONS ON THIS DRAWING SHALL BE CHECKED ON SITE BEFORE WORK COMMENCES.
 - FIGURED DIMENSIONS SHALL BE TAKEN IN PREFERENCE TO SCALE DIMENSIONS.
 - ALL DISCREPANCIES ARE TO BE REPORTED FOR CLARIFICATION BEFORE WORK COMMENCES.

REVISION NOTES		
DATE	DESCRIPTION	BY

JOB NO.
SCALE: 1/4" = 1'-0"

PREPARED BY.

DESCRIPTION .

CONCEPTUAL HOUSE PLAN

APPLICANT / OWNER.

ADDRESS.

79-299

DATE.
11-JUN-2026

SHEET NO.
A-02